ELEKTROSCHEMA

Projektbeschreibung:	Hauptverteilung Wohnung A
Objekt:	DEFH Klotenerstrasse 5 8304 Wallisellen
Kunde:	Glatt Homes GmbH Escherweg 3 8304 Wallisellen
Auftrags-Nummer:	24031
Schema-Nummer:	001

ansoplan
elektro–engineering

Index	Datum	Name	Erstellt	DNO
A	09.04.2026	DNO	Datum	02.11.2025
			Geprüft	
			Seite	1
			Druck	09.04.2026
Anzahl Seiten	19		26.0	20:55

TinLine GmbH

Inhaltsverzeichnis








Blatt	Bezeichnung 1	Bezeichnung 2	Index	Datum	Name
1	Deckblatt		A	09.04.2026	DNO
2	Inhaltsverzeichnis				
6	Anschluss- und	Umgebungsbedingungen			
7	Symbolverzeichnis				
8	Allgemeine Hinweise				
10	Einspeisung				
11	EVU, Lastabwurf		A	09.04.2026	DNO
20	Technikraum				
21	Technikraum		A	09.04.2026	DNO
22	Ladestation, Sauna, WM/TU UG		A	09.04.2026	DNO
23	Licht Technikraum, Untergeschoss				
24	Reserve, Garage, GWA				
25	Kochherd, Backofen, Steamer	Licht Wohnzimmer, Esszimmer			
26	Licht WC, Reduit, Schlafzimmer OG	Waschmaschine/Tumbler OG			
27	Licht Bad, Gang OG				
1000	Kabelliste				
1000.1	Kabelliste				
3000	Klemmenliste				
3000.1	Klemmenliste				

Anschluss- und Umgebungsbedingungen

Schaltgerätekombination nach SN EN 61439

Bemessungsspannung:	3x400V / 230V, 50Hz
Bemessungsstrom:	63A
Art des Netzes (Schutzmassnahmen):	☐ TN - C ☒ TN - S ☐ TN - C - S
Schutzart (Schrankgehäuse):	☐ IP30 ☐ IP40 ☐ IP54 ☒ IP31 ☐ IP41 ☐ IP....
Berührungsschutz:	☒ Zugang für Laien IP2xC ☐ Zugang für instruierte Personen IP2xB
Kurzschlussstrom an der Anschlussstelle:	☐ 4.5kA ☐ 10kA ☒ 6kA ☐ 20kA
Umgebungstemperatur:	☐ 20°C ☐ 35°C ☒ 25°C ☐ Eine Schrankbelüftung ist eventuell vorzusehen
Verschmutzungsgrad:	☒ 3 ☐ .
Besondere Anforderungen:	☐ .

Symbolverzeichnis

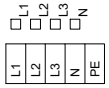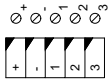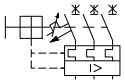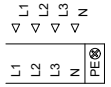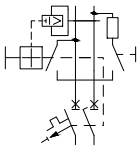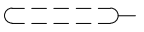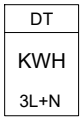 Leitungsschutzschalter	 Relais oder Schütz	 Digitale Uhr	 Hupe Allgemein	 Klemmen Normalspannung	
 Sicherung	 Anzugverzögertes Relais	 Analoge Uhr	 Wechselrichter	 Klemmen Kleinspannung	
 Leistungs- oder Motorschutz-Schalter	 Abfallverzögertes Relais	Widerstand	 Signalisationslampe	 Klemmen Direktabgang	
 Fehlerstrom-Schutzschalter mit Leitungs-Schutzschalter	Schliesskontakt	 Trafo	 Drehschalter	 Abschirmung	
	Öffnungskontakt	 Leuchtdiode	 Notschalter		
 Kilowatt-Stundenzähler	 Wechselkontakt	 Kondensator	 Schlüsselschalter		
	 Hauptkontakt	 Schutz-Erde			
 Voltmeter	 Anzugverzögerter Schliesskontakt	 Potentialquerverweis Abgehend nach			
 Ampèremeter	 Abfallverzögerter Schliesskontakt	 Potentialquerverweis Ankommend von			
 Motor	 Anzugverzögerter Wechselkontakt	 Thermometer			

Allgemeine Hinweise

1. Materialvorgaben

- Sind im Schema Vorgaben bezüglich Fabrikat, Typ und speziellen Eigenschaften vorgegeben, muss dieses Material verwendet werden.
- Abweichungen sind mit uns abzusprechen und gut zu heissen.
- Alle übrigen Materialien sind frei wählbar, sofern diese den aktuellen Normen- und Qualitätsstandards entsprechen.

2. Vorschriften / Prüfungen

- Örtliche Vorschriften (NIN, WV, SUVA, EN-Normen, UVG, Gebäude-Versicherungen) und Vorgaben Dritter sind zu berücksichtigen.
- Verteilungen >250A sind gemäss Norm EN 61439-1 und NIN 5.3.9 auszuführen und zu prüfen.
- Der Montageort ist auf Einhaltung der Brandschutzvorschriften zu prüfen.


3. Disposition

- Vor Erstellung sind die benötigten Mindestmasse der Verteilanlage mittels Grobdisposition des Planers bestätigen zu lassen. (inkl. Angabe Fabrikat, Typ, Masse, Farbe).
- Der Unternehmer/Lieferant ist verantwortlich für die Einbringung der Verteilanlagen in die dafür vorgesehenen Gebäude, Räume und Nischen. (Transportteilungen, Fluchtweg beachten).
- Die definitiven Masse sind am Bau aufzunehmen resp. zu kontrollieren.

4. Bezeichnungen

- Sämtliche Klemmen, Apparate, Bezeichnungsstreifen und Legenden sind mit identischen Beschriftungen gem. Schema zu kennzeichnen.
- Notberechtigte Abgänge sind in Legenden und Bezeichnungsstreifen sichtbar zu kennzeichnen.
- Not-Neutralleiter-Isolationen (hellblau) an den Enden grün bezeichnet.
- Prüfprotokolle und Legenden sind nach der Ausführungsphase zu bereinigen und auf der Anlage zu deponieren (Mit Kopie an Planer).
- Typenschilder sind gemäss den anerkannten Regeln der Technik und Regionalen Normen gut sichtbar und dauerhaft anzubringen.

5. Anlagespezifische Angaben

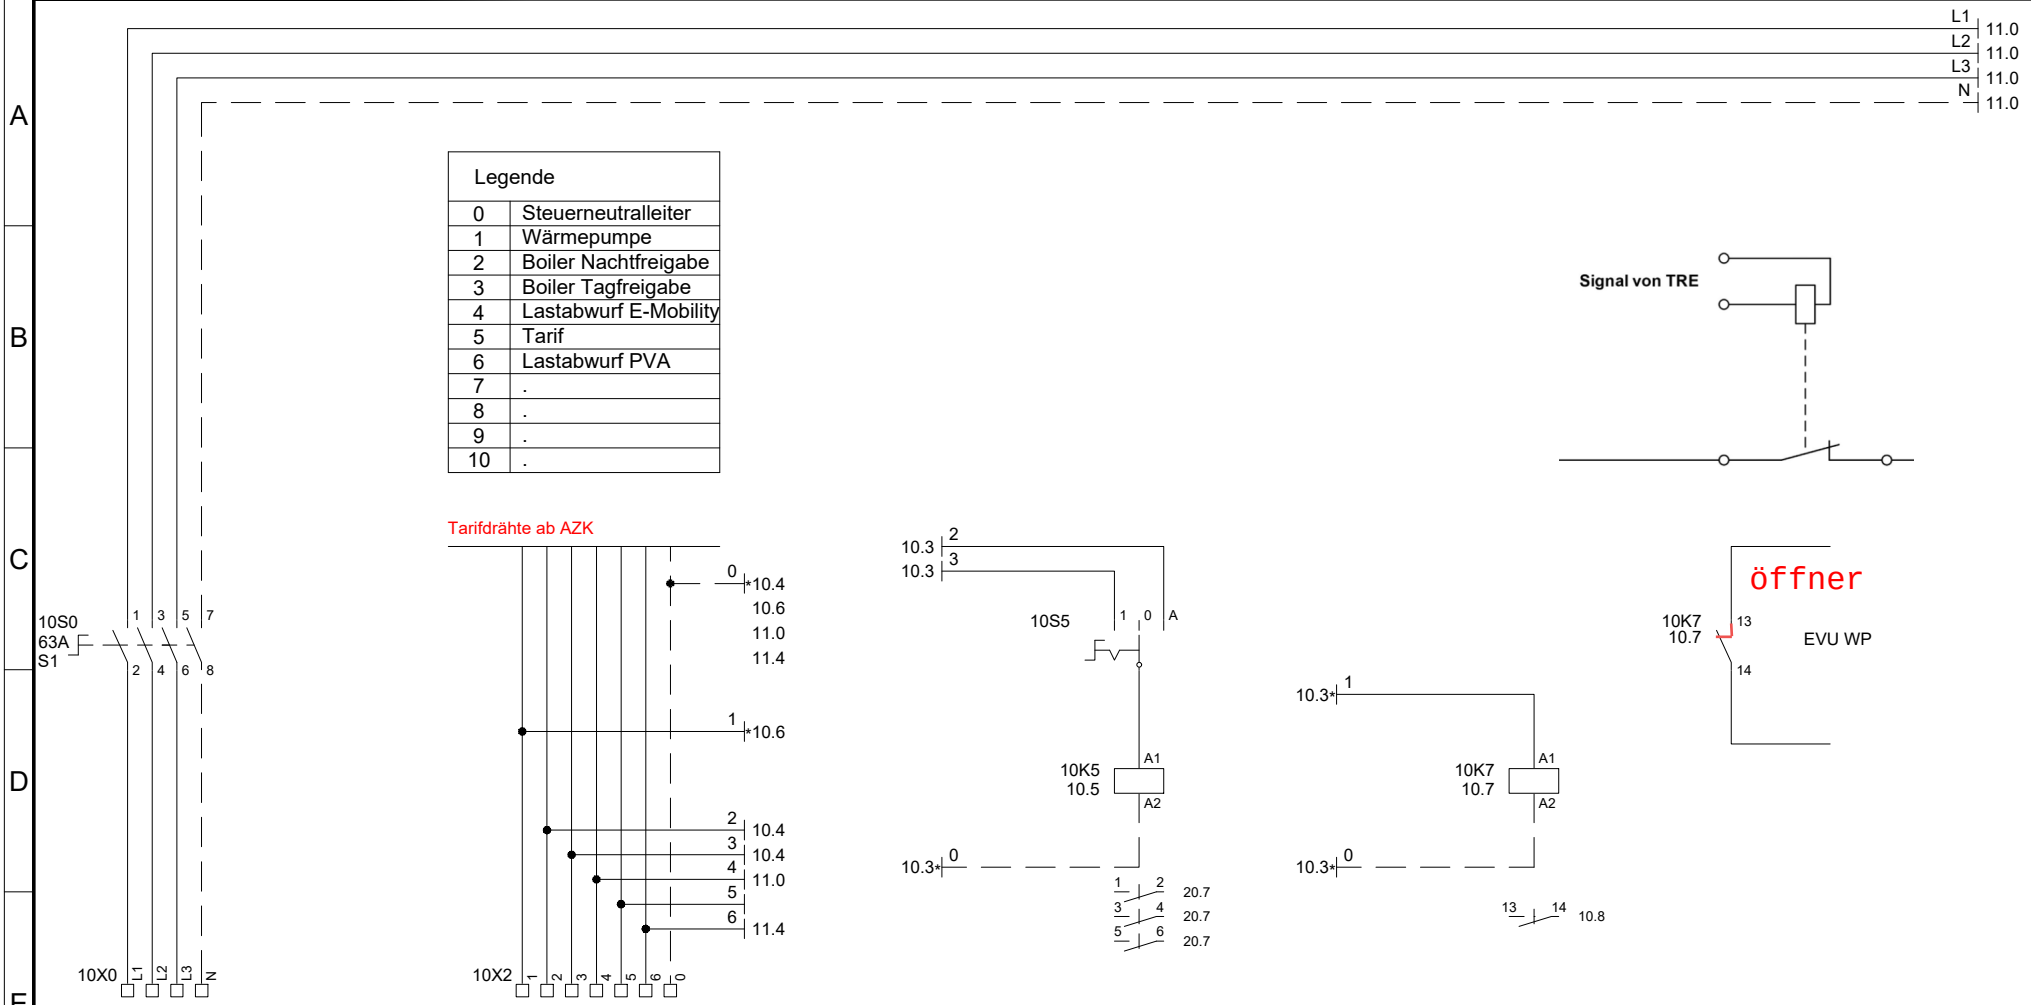

Index	Datum	Name	Gezeichnet
			DNO
			Erstelldatum
			02.11.2025

Hauptverteilung
Wohnung A


ansoplan
elektro-engineering

Einspeisung

Auftrag: 24031
Schema: 001

Seite 10
< 8 | 11 >

TinLine GmbH

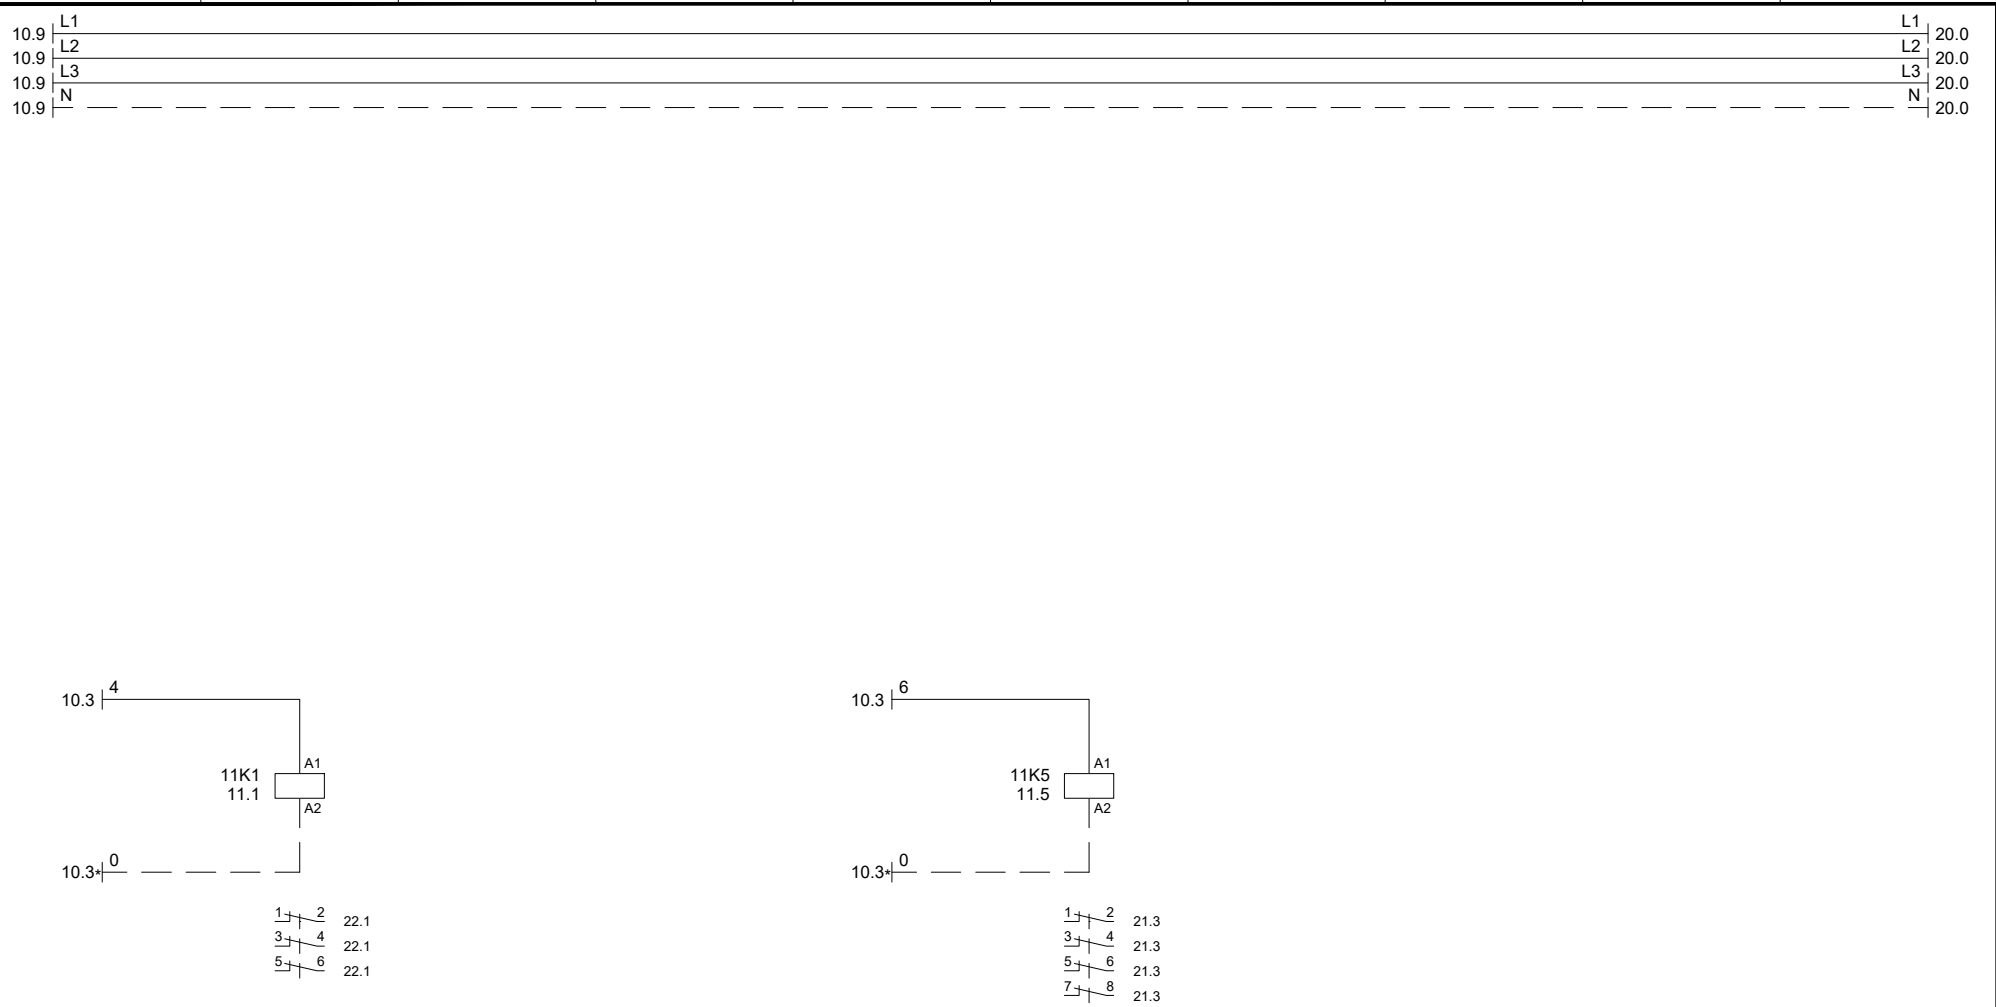

Index	Datum	Name	Gezeichnet
A	09.04.2026	DNO	DNO
			Erstelldatum
			02.11.2025

Hauptverteilung
Wohnung A


ansoplan
elektro-engineering

EVU, Lastabwurf

Auftrag: 24031
Schema: 001

Seite 11
< 10 | 20 >

TinLine GmbH

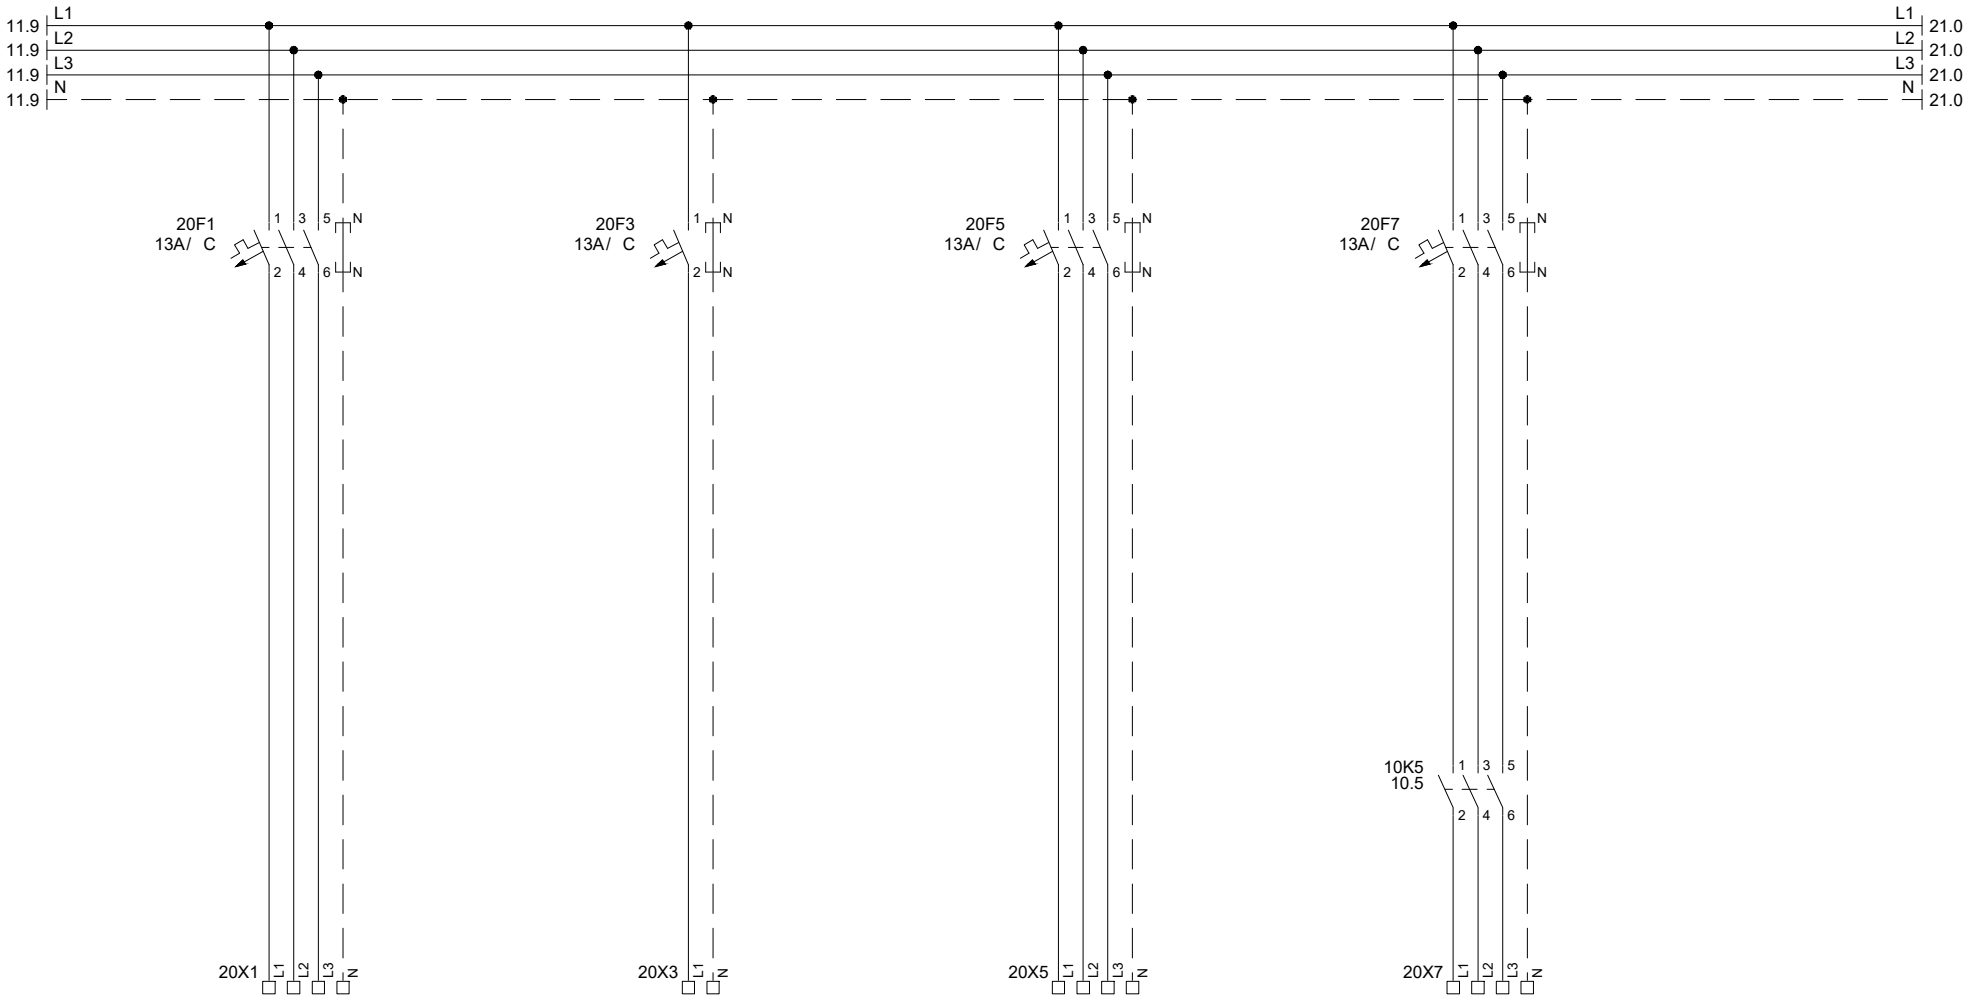


2.5mm²	2.5mm²	2.5mm²	2.5mm²
20X1	20X3	20X5	20X7
L1 L2 L3 N PE	L1 N PE	L1 L2 L3 N PE	L1 L2 L3 N PE
Wärmepumpe	Steuerung Wärmepumpe	Hebeanlage	Notheizung
FE0 5x1.5mm²	FE0 3x1.5mm²	FE0 5x1.5mm²	FE0 5x1.5mm²

Index	Datum	Name				
			Gezeichnet DNO	Hauptverteilung Wohnung A	ansoplan elektro-engineering	Technikraum
			Erstelldatum 02.11.2025			

Auftrag: 24031 Seite 20
Schema: 001 < 11 21 >

TinLine GmbH

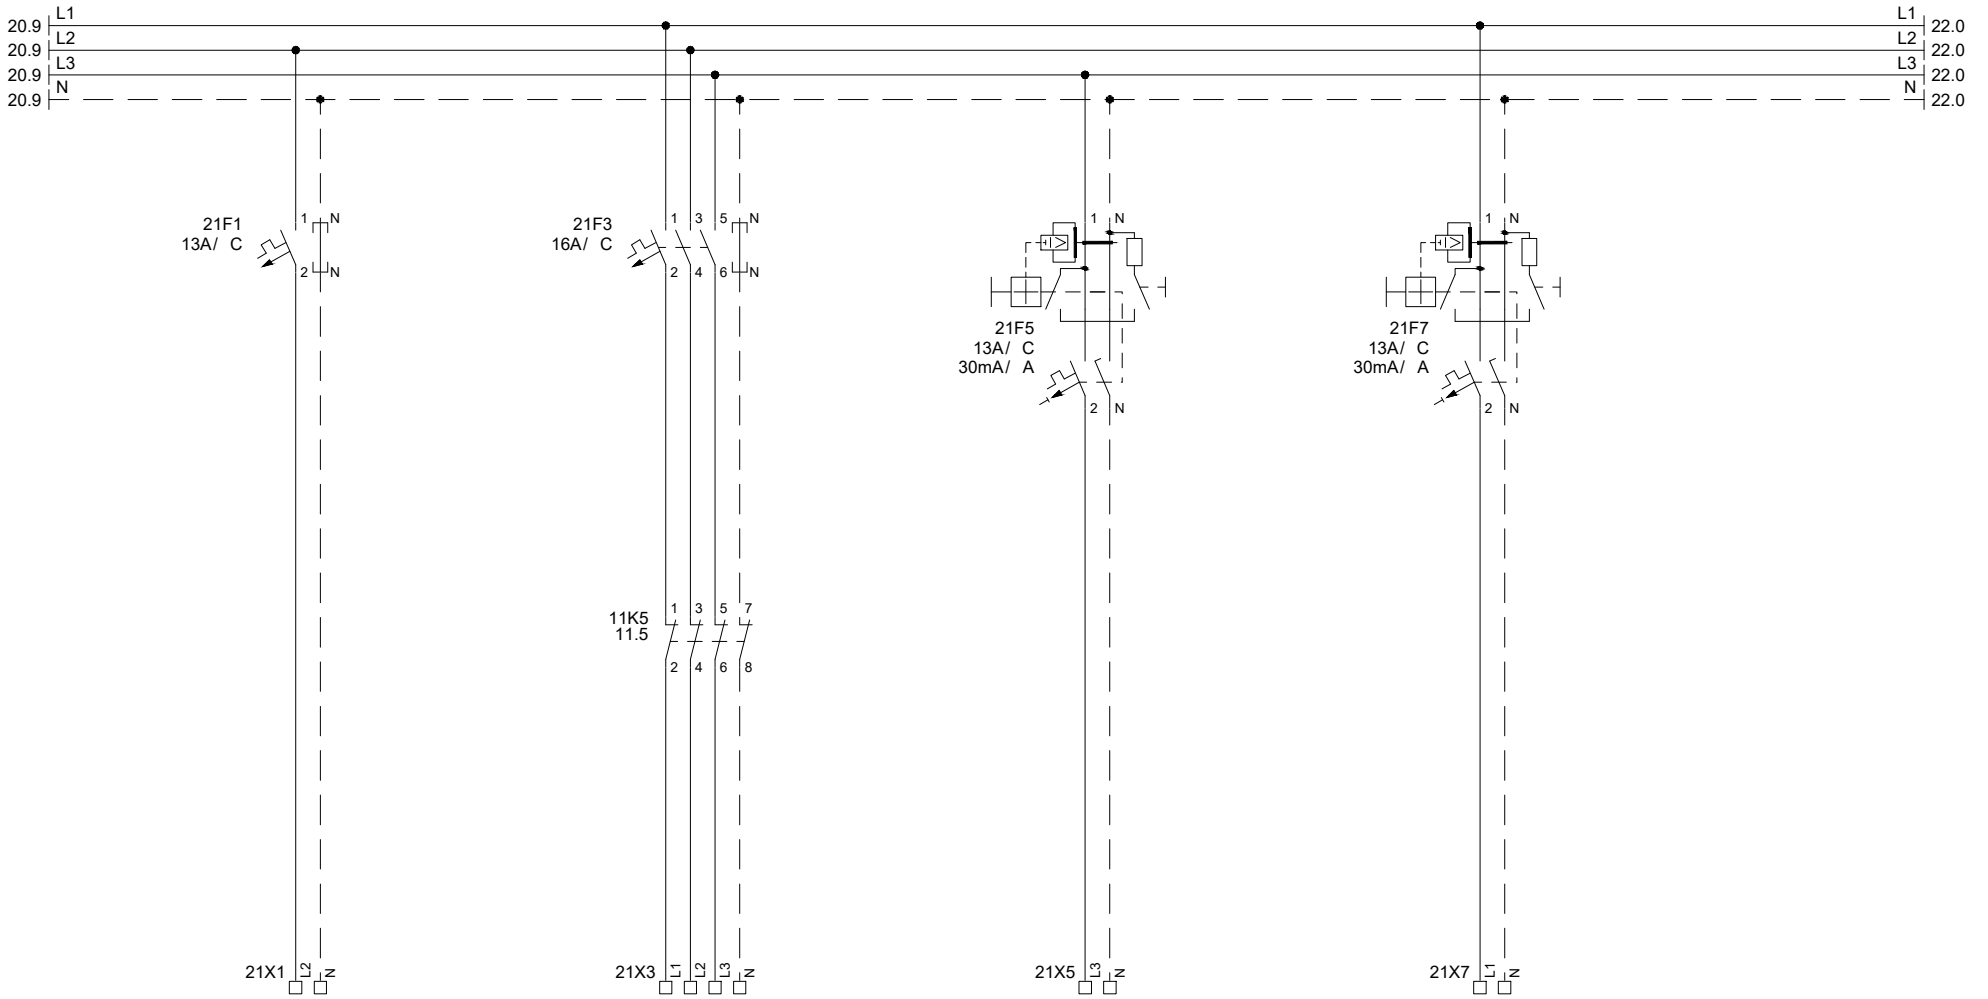

2.5mm²	2.5mm²	2.5mm²	2.5mm²
21X1	21X3	21X5	21X7
L2 N PE	L1 L2 L3 N PE	L3 N PE	L1 N PE
Zirkulationspumpe	Wechselrichter	HZV UG	HZV EG
FE0 3x1.5mm²	FE0 5x2.5mm²	FE0 3x1.5mm²	FE0 3x1.5mm²

Index	Datum	Name	Gezeichnet
A	09.04.2026	DNO	DNO
			Erstelldatum 02.11.2025

Hauptverteilung
Wohnung A


ansoplan elektro-engineering

Technikraum

Auftrag: 24031
Schema: 001

Seite 21
< 20 | 22 >

TinLine GmbH

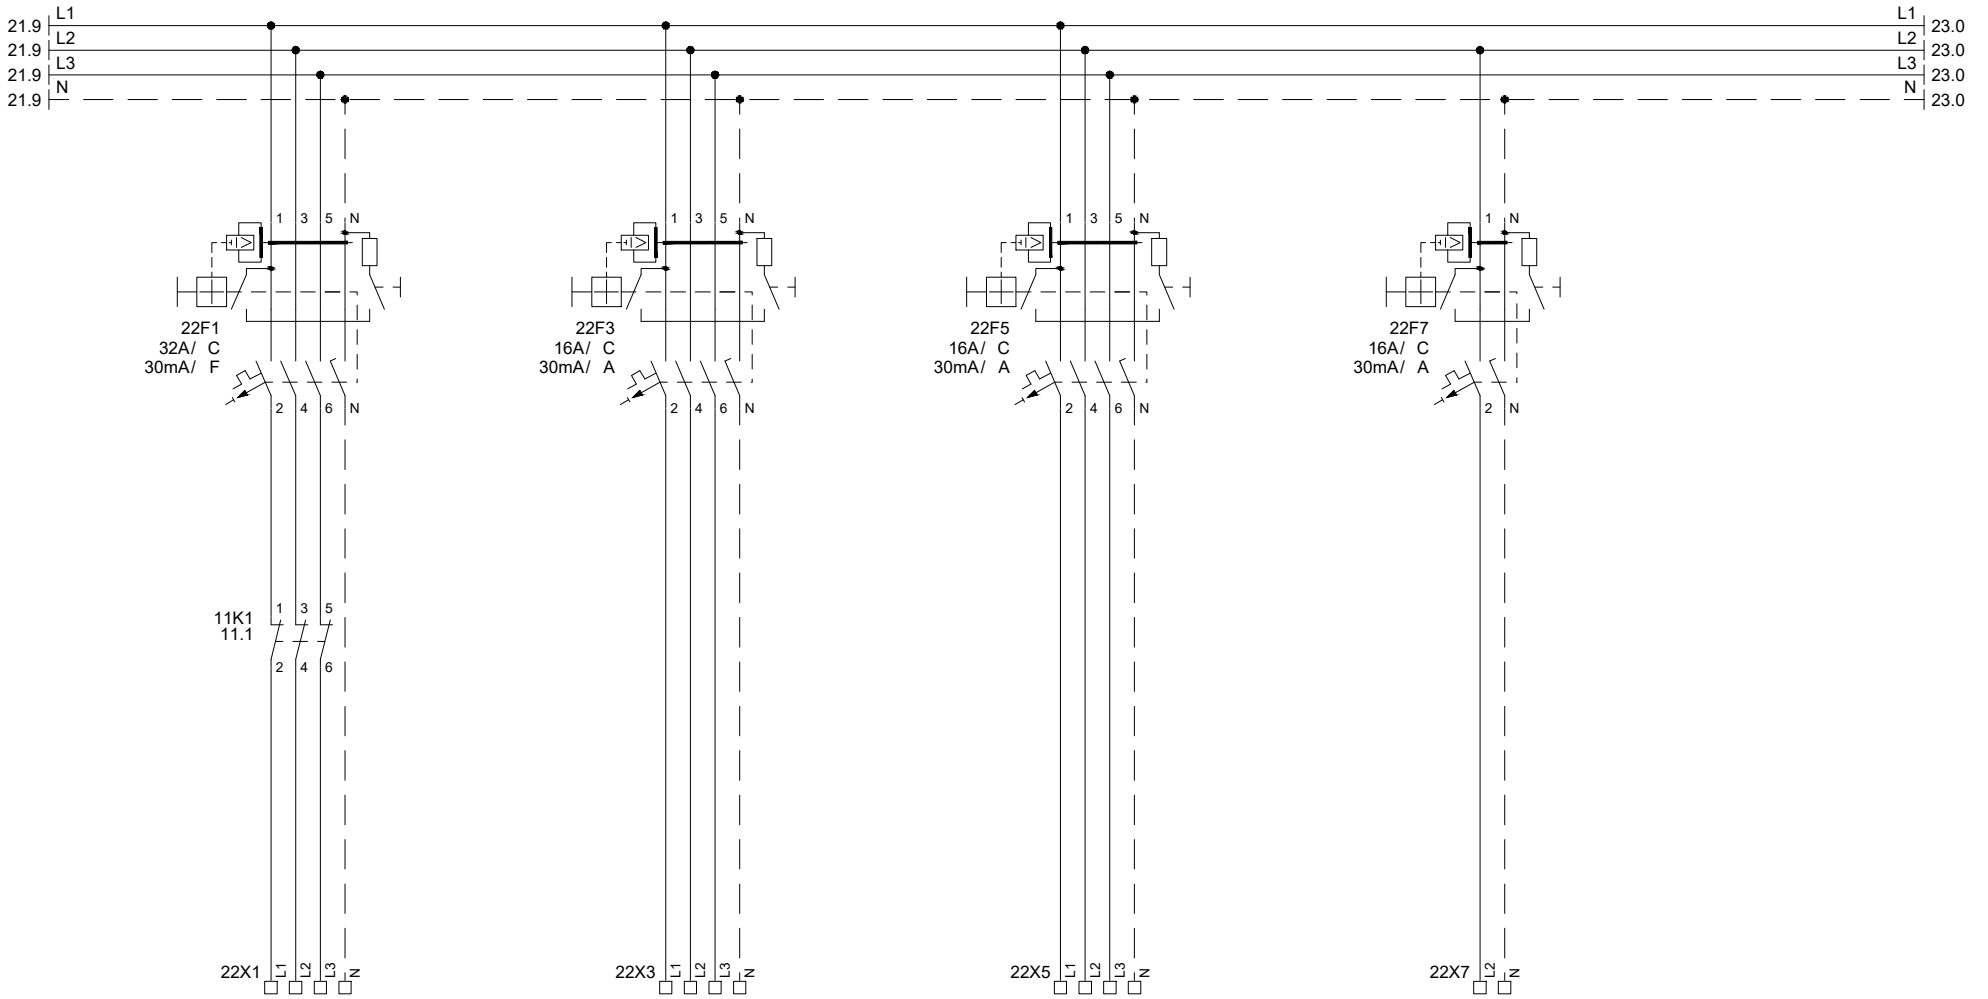

Index	Datum	Name	Gezeichnet
A	09.04.2026	DNO	DNO
			Erstelldatum 02.11.2025

Hauptverteilung
Wohnung A


ansoplan elektro-engineering

Ladestation, Sauna, WM/TU UG

Auftrag: 24031
Schema: 001

Seite 22
< 21 | 23 >

TinLine GmbH

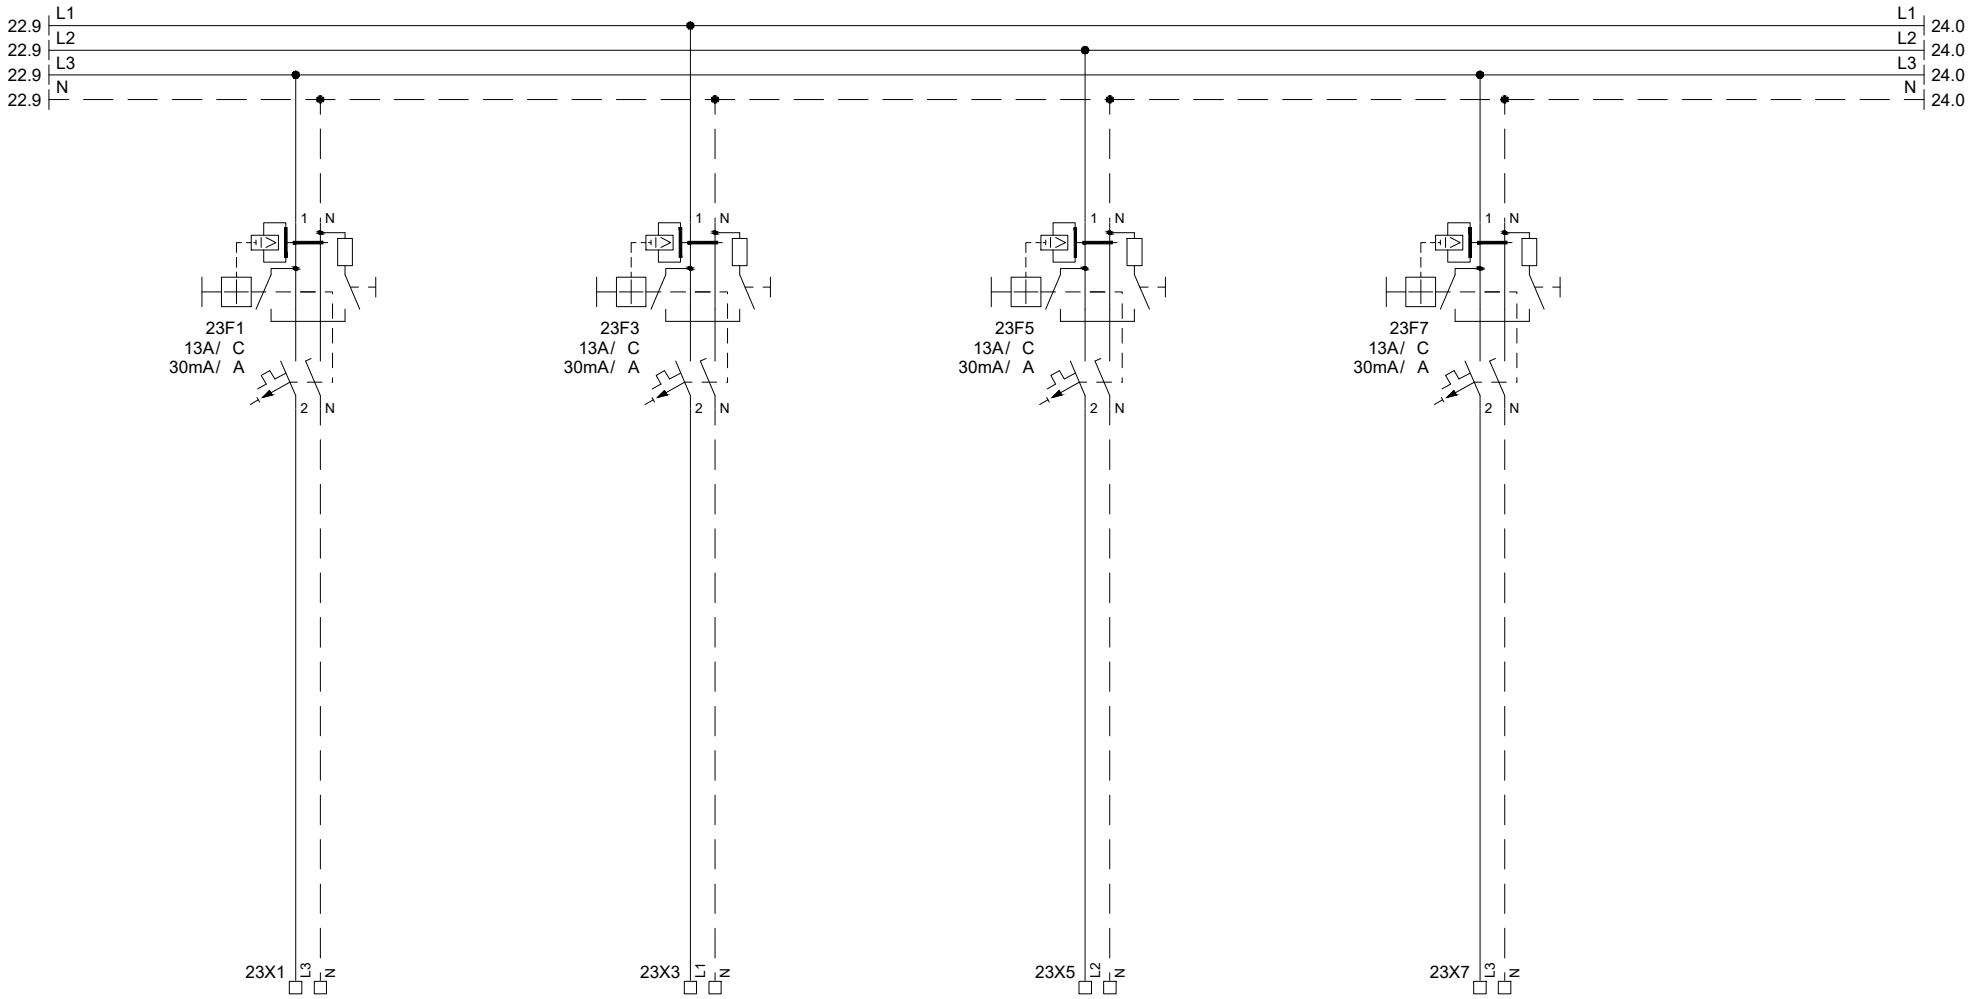

	23X1	23X3	23X5	23X7
	2.5mm²	2.5mm²	2.5mm²	2.5mm²
	L3 N PE	L1 N PE	L2 N PE	L3 N PE
	Rack 3xT13	Schlafzimmer 1+2 UG	Technikraum Keller	Bad, Gang UG
	FE0 3x1.5mm²	FE0 3x1.5mm²	FE0 3x1.5mm²	FE0 3x1.5mm²

Index	Datum	Name	Gezeichnet
			DNO
			Erstelldatum
			02.11.2025

Hauptverteilung
Wohnung A


ansoplan
elektro-engineering

Licht Technikraum, Untergeschoss

Auftrag: 24031
Schema: 001

Seite 23
< 22 | 24 >

TinLine GmbH

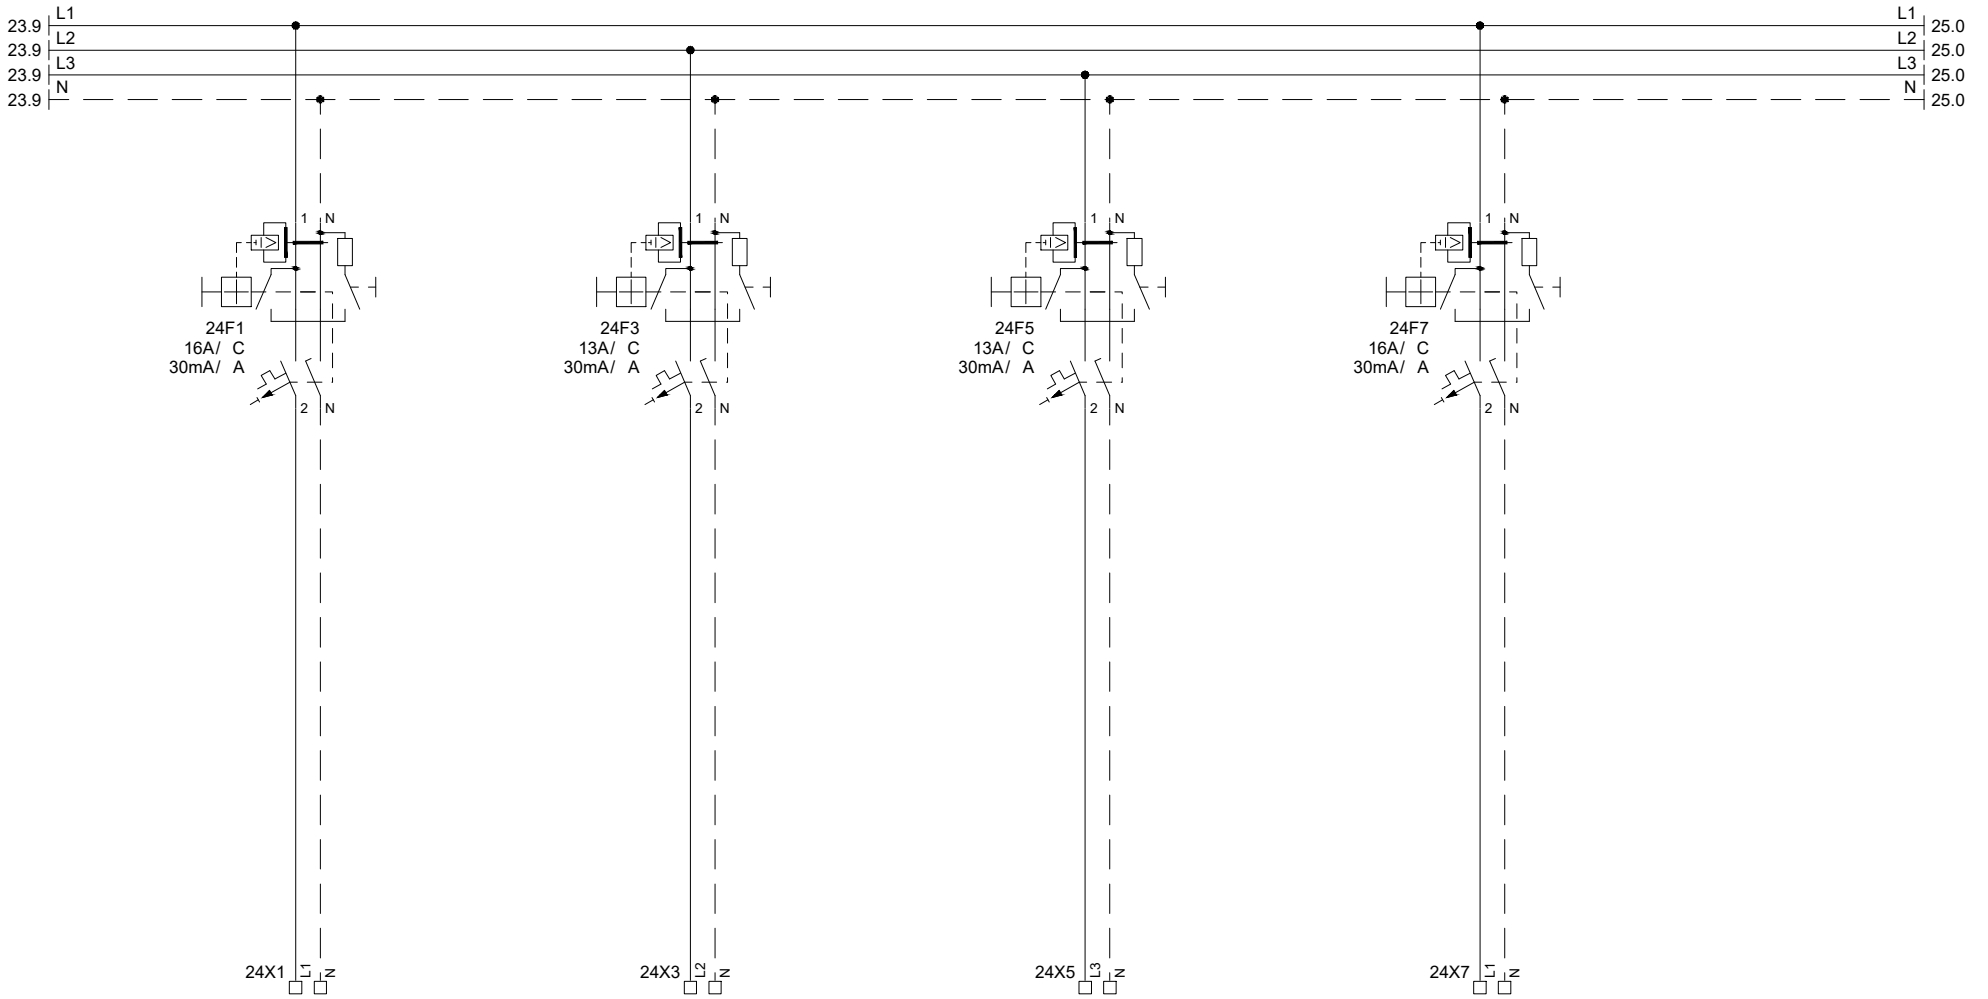

2.5mm²	2.5mm²	2.5mm²	2.5mm²
24X1	24X3	24X5	24X7
L1 N PE	L2 N PE	L3 N PE	L1 N PE
Reserve (Rohrbegleitheizung)	Reserve	Garage	GWA
FE0 3x2.5mm²	FE0 3x1.5mm²	FE0 3x1.5mm²	FE0 3x2.5mm²

Index	Datum	Name	Gezeichnet
			DNO
			Erstelldatum
			02.11.2025

Hauptverteilung
Wohnung A


ansoplan
elektro-engineering

Reserve, Garage, GWA

Auftrag: 24031
Schema: 001

Seite 24
< 23 | 25 >

TinLine GmbH

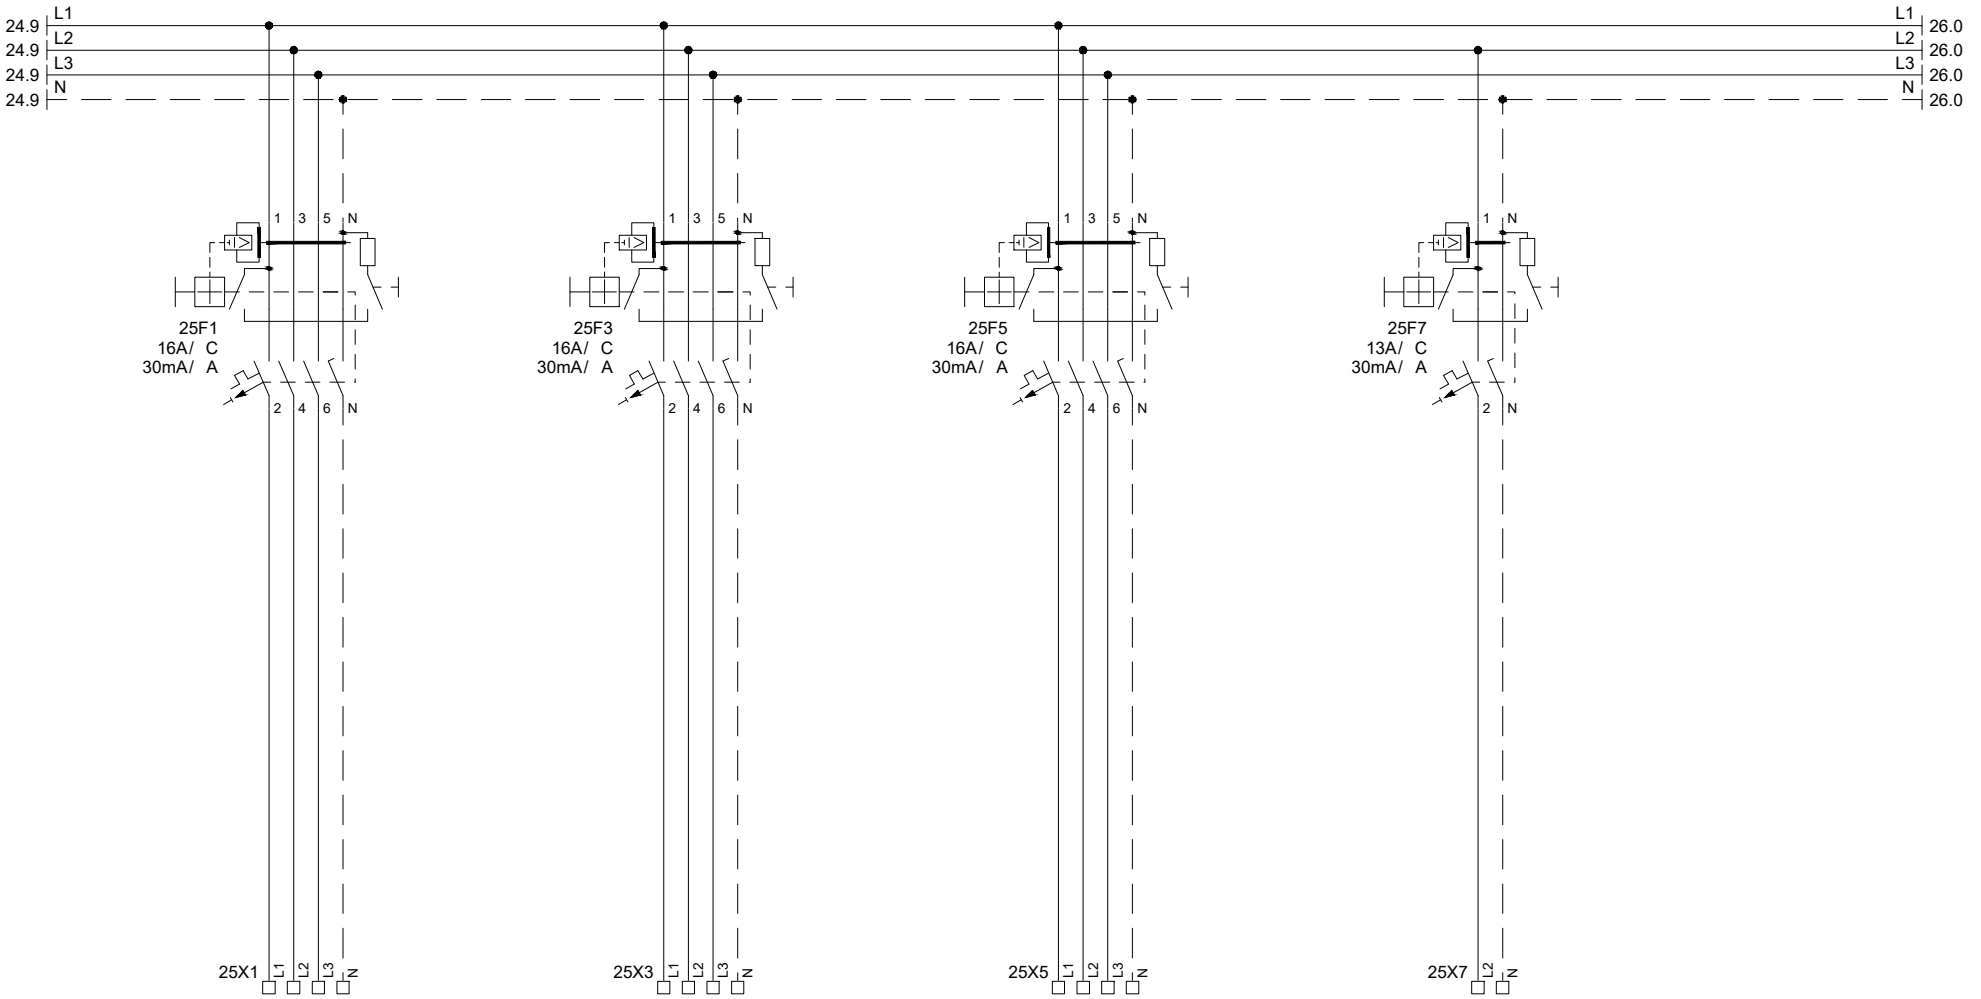

2.5mm²	2.5mm²	2.5mm²	2.5mm²
25X1	25X3	25X5	25X7
L1 L2 L3 N PE	L1 L2 L3 N PE	L1 L2 L3 N PE	L2 N PE
Kochherd	Backofen	Steamer	Wohnzimmer Esszimmer
FE0 5x2.5mm²	FE0 5x2.5mm²	FE0 5x2.5mm²	FE0 3x1.5mm²

TinLine GmbH

Index	Datum	Name	Gezeichnet
			DNO
			Erstelldatum
			02.11.2025


Hauptverteilung
Wohnung A

ansoplan
elektro-engineering

Kochherd, Backofen, Steamer
Licht Wohnzimmer, Esszimmer

Auftrag: 24031
Schema: 001

Seite 25
< 24 | 26 >

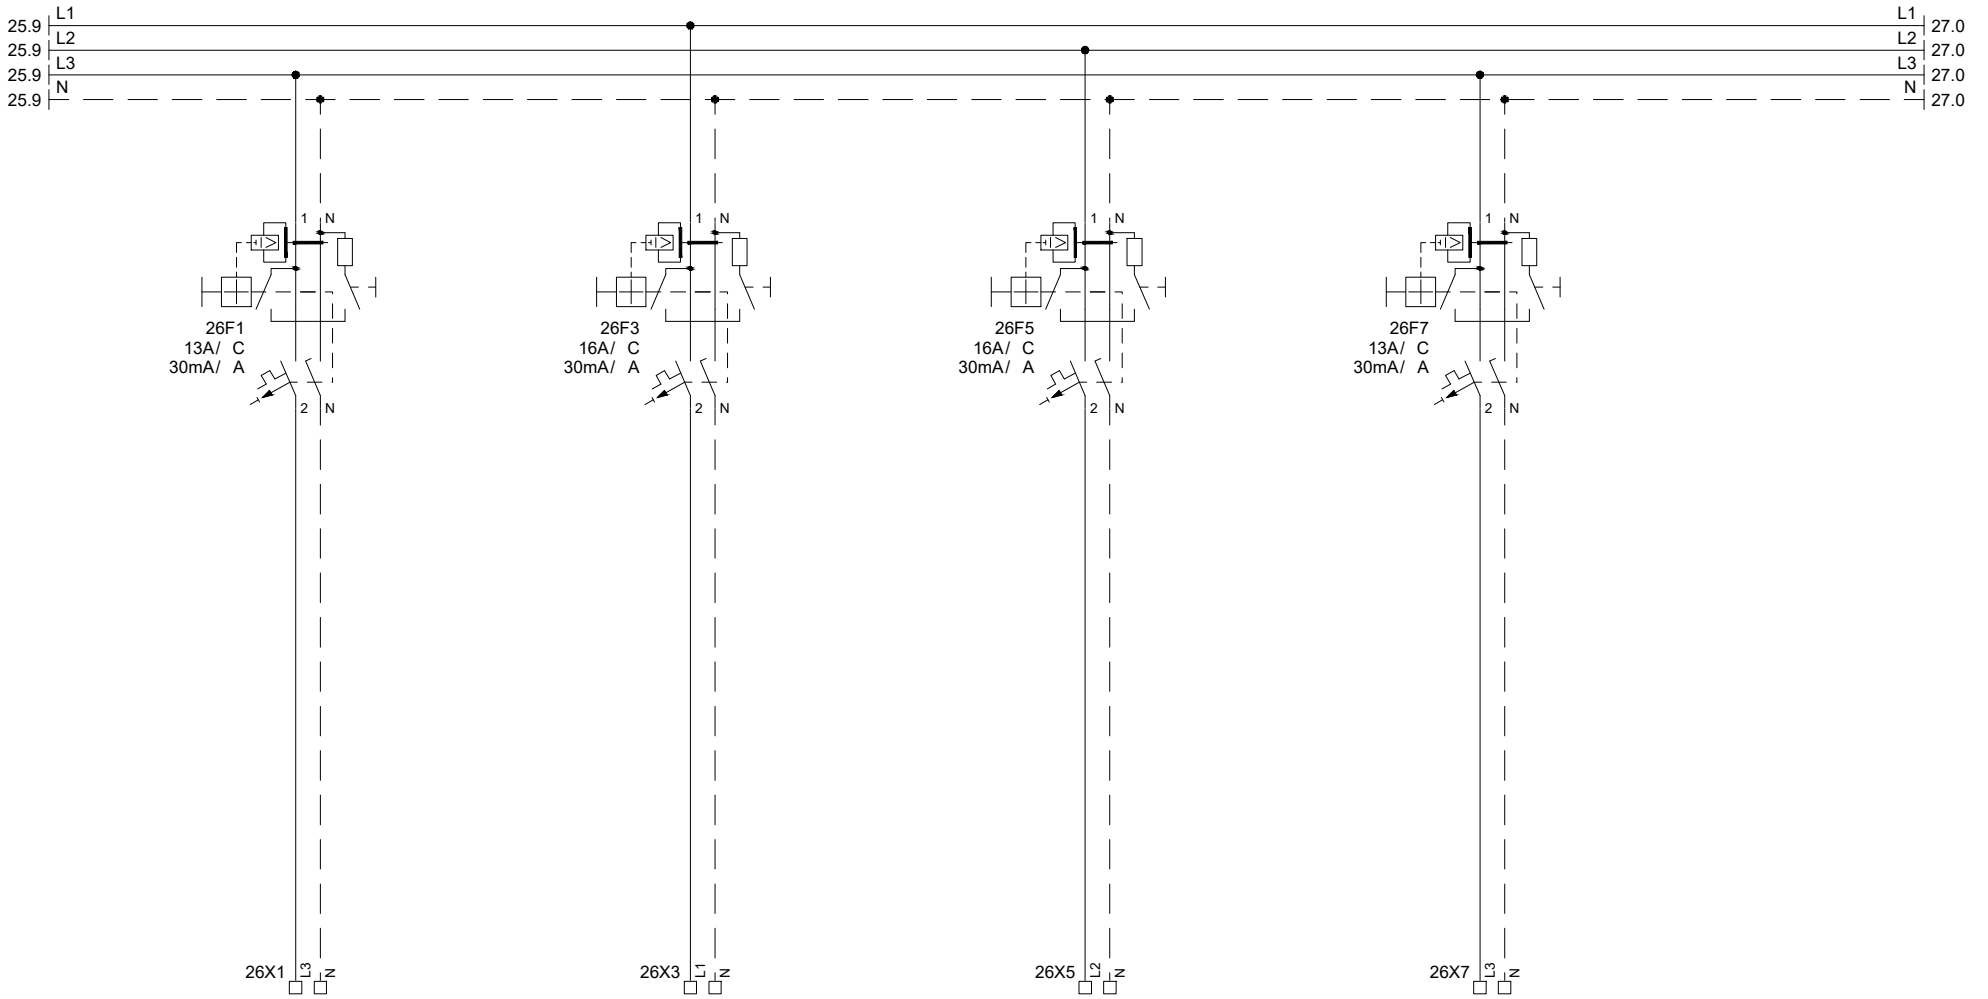

	26X1	26X3	26X5	26X7
	2.5mm²	2.5mm²	2.5mm²	2.5mm²
	L3 N PE	L1 N PE	L2 N PE	L3 N PE
	WC Reduit	Waschmaschine OG	Tumbler OG	Schlafzimmer OG
	FE0 3x1.5mm²	FE0 3x2.5mm²	FE0 3x2.5mm²	FE0 3x1.5mm²

Index	Datum	Name	Gezeichnet
			DNO
			Erstelldatum
			02.11.2025

Hauptverteilung
Wohnung A


ansoplan
elektro-engineering

Licht WC, Reduit, Schlafzimmer OG
Waschmaschine/Tumbler OG

Auftrag: 24031
Schema: 001

Seite 26
< 25 | 27 >

TinLine GmbH

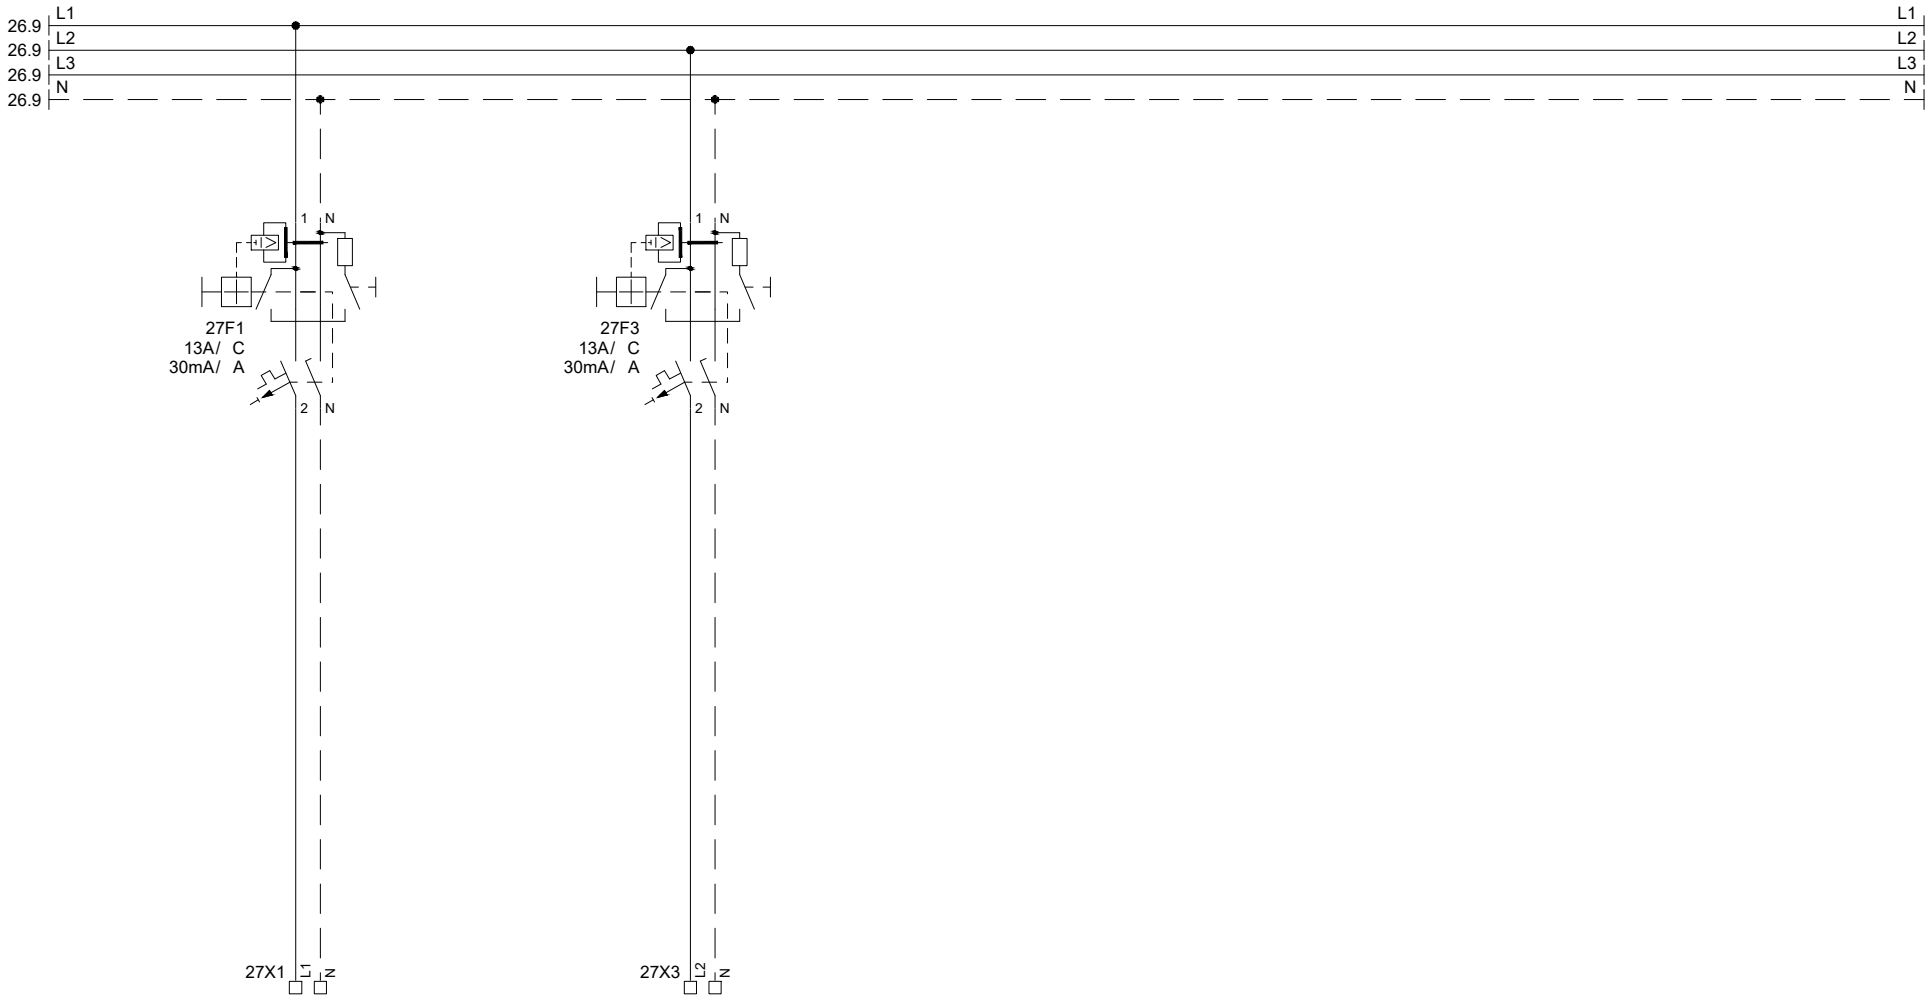

2.5mm²	2.5mm²
27X1	27X3
L1 N PE	L2 N PE
Bad OG Gang OG	Reserve
FE0 3x1.5mm²	FE0 3x1.5mm²

Index	Datum	Name	Gezeichnet
			DNO
			Erstelldatum
			02.11.2025

Hauptverteilung
Wohnung A

ansoplan
elektro-engineering

Licht Bad, Gang OG

Auftrag: 24031
Schema: 001

Seite 27
< 26 | 1000 >

TinLine GmbH

Kabelliste

BMK	Kabel	Leistung	Bezeichnung / Abgang
10X0	FE0 5x16mm²		Zuleitung ab AZK
10X2	FE0 7x1.5mm²		Klemmen für Tarifdrähte ab NKE AZK Plombierbar
20X1	FE0 5x1.5mm²		Wärmepumpe
20X3	FE0 3x1.5mm²		Steuerung Wärmepumpe
20X5	FE0 5x1.5mm²		Hebeanlage
20X7	FE0 5x1.5mm²		Notheizung
21X1	FE0 3x1.5mm²		Zirkulationspumpe
21X3	FE0 5x2.5mm²		Wechselrichter
21X5	FE0 3x1.5mm²		HZV UG
21X7	FE0 3x1.5mm²		HZV EG
22X1	FE0 5x10mm²		Ladestation
22X3	FE0 5x2.5mm²		Sauna
22X5	FE0 5x2.5mm²		Waschmaschine
22X7	FE0 3x2.5mm²		Tumbler
23X1	FE0 3x1.5mm²		Rack 3xT13
23X3	FE0 3x1.5mm²		Schlafzimmer 1+2 UG
23X5	FE0 3x1.5mm²		Technikraum Keller
23X7	FE0 3x1.5mm²		Bad, Gang UG
24X1	FE0 3x2.5mm²		Reserve (Rohrbegleitheizung)
24X3	FE0 3x1.5mm²		Reserve
24X5	FE0 3x1.5mm²		Garage
24X7	FE0 3x2.5mm²		GWA
25X1	FE0 5x2.5mm²		Kochherd
25X3	FE0 5x2.5mm²		Backofen
25X5	FE0 5x2.5mm²		Steamer
25X7	FE0 3x1.5mm²		Wohnzimmer Esszimmer
26X1	FE0 3x1.5mm²		WC Reduit
26X3	FE0 3x2.5mm²		Waschmaschine OG
26X5	FE0 3x2.5mm²		Tumbler OG
26X7	FE0 3x1.5mm²		Schlafzimmer OG

Kabelliste

BMK	Kabel	Leistung	Bezeichnung / Abgang
27X1	FE0 3x1.5mm²		Bad OG Gang OG

Index	Datum	Name	Gezeichnet
			DNO
			Erstelldatum
			02.11.2025

Hauptverteilung
Wohnung A

ansoplan
elektro-engineering

Kabelliste

Auftrag: 24031
Schema: 001

Seite 1000.1
< 1000 | 3000 >

TinLine GmbH

Klemmenliste

BMK	Kabel	Bezeichnung / Abgang	1	2	3	4	5	6	7	8	9	10
10X0	FE0 5x16mm²	Zuleitung ab AZK	L1	L2	L3	N	PE					
10X2	FE0 7x1.5mm²	Klemmen für Tarifdrähte ab NKE AZK Plombierbar	1	2	3	4	5	6	0			
20X1	FE0 5x1.5mm²	Wärmepumpe	L1	L2	L3	N	PE					
20X3	FE0 3x1.5mm²	Steuerung Wärmepumpe	L1	N	PE							
20X5	FE0 5x1.5mm²	Hebeanlage	L1	L2	L3	N	PE					
20X7	FE0 5x1.5mm²	Notheizung	L1	L2	L3	N	PE					
21X1	FE0 3x1.5mm²	Zirkulationspumpe	L2	N	PE							
21X3	FE0 5x2.5mm²	Wechselrichter	L1	L2	L3	N	PE					
21X5	FE0 3x1.5mm²	HZV UG	L3	N	PE							
21X7	FE0 3x1.5mm²	HZV EG	L1	N	PE							
22X1	FE0 5x10mm²	Ladestation	L1	L2	L3	N	PE					
22X3	FE0 5x2.5mm²	Sauna	L1	L2	L3	N	PE					
22X5	FE0 5x2.5mm²	Waschmaschine	L1	L2	L3	N	PE					
22X7	FE0 3x2.5mm²	Tumbler	L2	N	PE							
23X1	FE0 3x1.5mm²	Rack 3xT13	L3	N	PE							
23X3	FE0 3x1.5mm²	Schlafzimmer 1+2 UG	L1	N	PE							
23X5	FE0 3x1.5mm²	Technikraum Keller	L2	N	PE							
23X7	FE0 3x1.5mm²	Bad, Gang UG	L3	N	PE							
24X1	FE0 3x2.5mm²	Reserve (Rohrbegleitheizung)	L1	N	PE							
24X3	FE0 3x1.5mm²	Reserve	L2	N	PE							
24X5	FE0 3x1.5mm²	Garage	L3	N	PE							
24X7	FE0 3x2.5mm²	GWA	L1	N	PE							
25X1	FE0 5x2.5mm²	Kochherd	L1	L2	L3	N	PE					
25X3	FE0 5x2.5mm²	Backofen	L1	L2	L3	N	PE					
25X5	FE0 5x2.5mm²	Steamer	L1	L2	L3	N	PE					
25X7	FE0 3x1.5mm²	Wohnzimmer Esszimmer	L2	N	PE							
26X1	FE0 3x1.5mm²	WC Reduit	L3	N	PE							
26X3	FE0 3x2.5mm²	Waschmaschine OG	L1	N	PE							
26X5	FE0 3x2.5mm²	Tumbler OG	L2	N	PE							
26X7	FE0 3x1.5mm²	Schlafzimmer OG	L3	N	PE							

Klemmenliste

BMK	Kabel	Bezeichnung / Abgang	1	2	3	4	5	6	7	8	9	10
27X1	FE0 3x1.5mm²	Bad OG Gang OG	L1	N	PE							

Index	Datum	Name	Gezeichnet	Hauptverteilung	ansoplan elektro-engineering	Klemmenliste	Auftrag:	24031	Seite 3000.1
			DNO						
			Erstelldatum 02.11.2025	Wohnung A			Schema:	001	< 3000 >

TinLine GmbH