ELEKTROSCHEMA

Projektbeschreibung:	Hauptverteilung Wohnung B
Objekt:	DEFH Klotenerstrasse 5 8304 Wallisellen
Kunde:	Glatt Homes GmbH Escherweg 3 8304 Wallisellen
Auftrags-Nummer:	24031
Schema-Nummer:	001

ansoplan
elektro–engineering

TinLine GmbH

Index	Datum	Name	Erstellt	DNO
			Datum	02.11.2025
			Geprüft	
			Seite	1
			Druck	09.04.2026
Anzahl Seiten	15		26.0	20:50

Inhaltsverzeichnis









Blatt	Bezeichnung 1	Bezeichnung 2	Index	Datum	Name
1	Deckblatt				
2	Inhaltsverzeichnis				
6	Anschluss- und	Umgebungsbedingungen			
7	Symbolverzeichnis				
8	Allgemeine Hinweise				
10	Einspeisung				
11	EVU, Lastabwurf		A	09.04.2026	DNO
20	Technikraum, Waschmaschine				
21	Technikraum		A	09.04.2026	DNO
22	Licht Technikraum, Untergeschoss				
23	Reserve, Garage, GWA				
24	Kochherd, Backofen, Steamer	Licht Wohnzimmer, Esszimmer			
25	Licht WC, Schlafzimmer OG				
1000	Kabelliste				
3000	Klemmenliste				

Anschluss- und Umgebungsbedingungen

Schaltgerätekombination nach SN EN 61439

Bemessungsspannung:	3x400V / 230V, 50Hz
Bemessungsstrom:	40A
Art des Netzes (Schutzmassnahmen):	☐ TN - C ☒ TN - S ☐ TN - C - S
Schutzart (Schrankgehäuse):	☐ IP30 ☐ IP40 ☐ IP54 ☒ IP31 ☐ IP41 ☐ IP....
Berührungsschutz:	☒ Zugang für Laien IP2xC ☐ Zugang für instruierte Personen IP2xB
Kurzschlussstrom an der Anschlussstelle:	☐ 4.5kA ☐ 10kA ☒ 6kA ☐ 20kA
Umgebungstemperatur:	☐ 20°C ☐ 35°C ☒ 25°C ☐ Eine Schrankbelüftung ist eventuell vorzusehen
Verschmutzungsgrad:	☒ 3 ☐ .
Besondere Anforderungen:	☐ .

Symbolverzeichnis

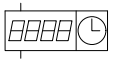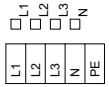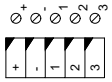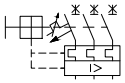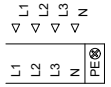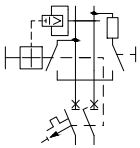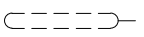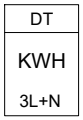 Leitungsschutzschalter	 Relais oder Schütz	 Digitale Uhr	 Hupe Allgemein	 Klemmen Normalspannung	
 Sicherung	 Anzugverzögertes Relais	 Analoge Uhr	 Wechselrichter	 Klemmen Kleinspannung	
 Leistungs- oder Motorschutz-Schalter	 Abfallverzögertes Relais	Widerstand	 Signalisationslampe	 Klemmen Direktabgang	
 Fehlerstrom-Schutzschalter mit Leitungs-Schutzschalter	Schliesskontakt	 Trafo	 Drehschalter	 Abschirmung	
	Öffnungskontakt	 Leuchtdiode	 Notschalter		
 Kilowatt-Stundenzähler	 Wechselkontakt	 Kondensator	 Schlüsselschalter		
	 Hauptkontakt	 Schutz-Erde			
 Voltmeter	 Anzugverzögerter Schliesskontakt	 Potentialquerverweis Abgehend nach			
 Ampèremeter	 Abfallverzögerter Schliesskontakt	 Potentialquerverweis Ankommend von			
 Motor	 Anzugverzögerter Wechselkontakt	 Thermometer			

Index	Datum	Name	Gezeichnet	Hauptverteilung	ansoplan elektro-engineering	Symbolverzeichnis	Auftrag: 24031	Seite 7
			DNO	Wohnung B			Schema: 001	< 6 / 8 >
			Erstelldatum 02.11.2025					

TinLine GmbH

Allgemeine Hinweise

1. Materialvorgaben

- Sind im Schema Vorgaben bezüglich Fabrikat, Typ und speziellen Eigenschaften vorgegeben, muss dieses Material verwendet werden.
- Abweichungen sind mit uns abzusprechen und gut zu heissen.
- Alle übrigen Materialien sind frei wählbar, sofern diese den aktuellen Normen- und Qualitätsstandards entsprechen.

2. Vorschriften / Prüfungen

- Örtliche Vorschriften (NIN, WV, SUVA, EN-Normen, UVG, Gebäude-Versicherungen) und Vorgaben Dritter sind zu berücksichtigen.
- Verteilungen >250A sind gemäss Norm EN 61439-1 und NIN 5.3.9 auszuführen und zu prüfen.
- Der Montageort ist auf Einhaltung der Brandschutzvorschriften zu prüfen.

3. Disposition


- Vor Erstellung sind die benötigten Mindestmasse der Verteilanlage mittels Grobdisposition des Planers bestätigen zu lassen. (inkl. Angabe Fabrikat, Typ, Masse, Farbe).
- Der Unternehmer/Lieferant ist verantwortlich für die Einbringung der Verteilanlagen in die dafür vorgesehenen Gebäude, Räume und Nischen. (Transportteilungen, Fluchtweg beachten).
- Die definitiven Masse sind am Bau aufzunehmen resp. zu kontrollieren.

4. Bezeichnungen

- Sämtliche Klemmen, Apparate, Bezeichnungsstreifen und Legenden sind mit identischen Beschriftungen gem. Schema zu kennzeichnen.
- Notberechtigte Abgänge sind in Legenden und Bezeichnungsstreifen sichtbar zu kennzeichnen.
- Not-Neutralleiter-Isolationen (hellblau) an den Enden grün bezeichnet.
- Prüfprotokolle und Legenden sind nach der Ausführungsphase zu bereinigen und auf der Anlage zu deponieren (Mit Kopie an Planer).
- Typenschilder sind gemäss den anerkannten Regeln der Technik und Regionalen Normen gut sichtbar und dauerhaft anzubringen.

5. Anlagespezifische Angaben


Legende	
0	Steuerneutralleiter
1	Wärmepumpe
2	Boiler Nachtfreigabe
3	Boiler Tagfreigabe
4	Lastabwurf E-Mobility
5	Tarif
6	Lastabwurf PVA
7	.
8	.
9	.
10	.

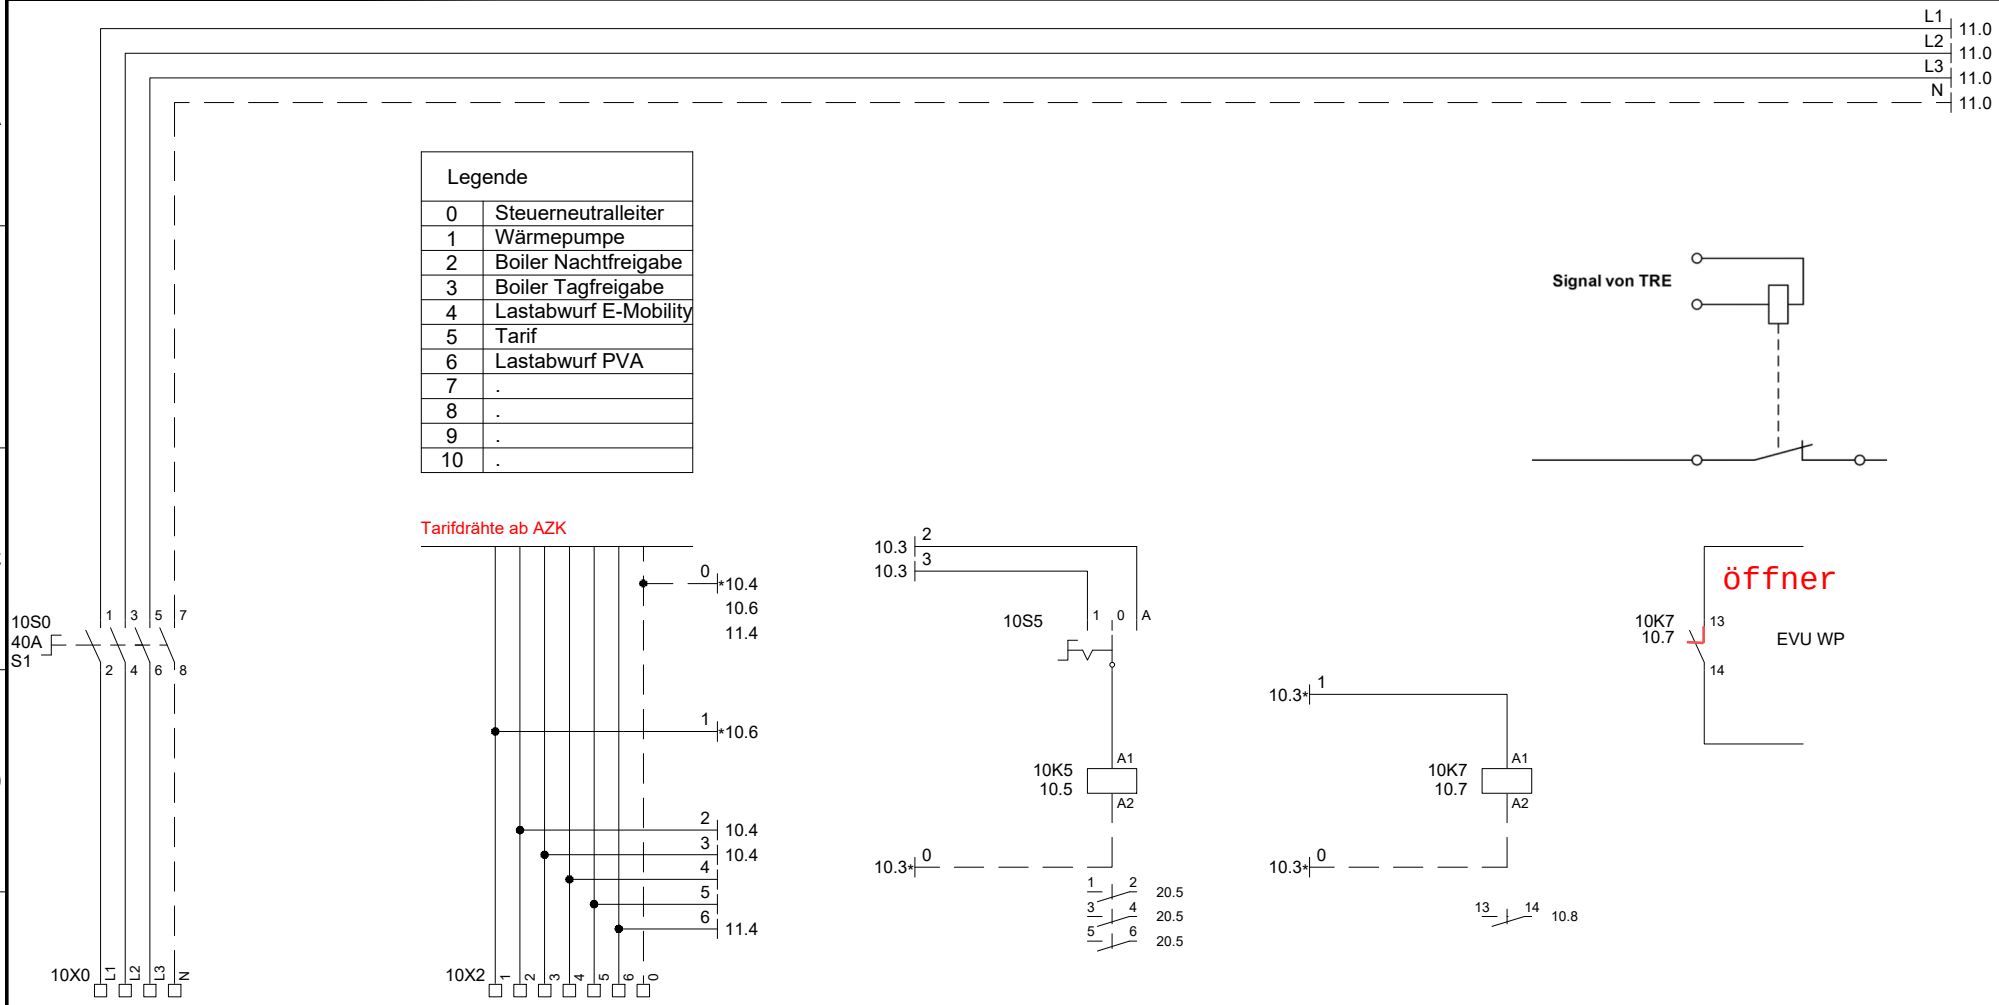

10mm²	2.5mm²
10X0	10X2
L1 L2 L3 N PE	1 2 3 4 5 6 0
Zuleitung ab AZK FE0 5x10mm²	Klemmen für Tarifdrähte ab NKE AZK Plombierbar FE0 7x1.5mm²

Index	Datum	Name	Gezeichnet	Hauptverteilung	ansoplan elektro-engineering	Einspeisung	Auftrag: 24031	Seite 10
			DNO	Wohnung B			Schema: 001	< 8 / 11 >
			Erstelldatum 02.11.2025					

TinLine GmbH

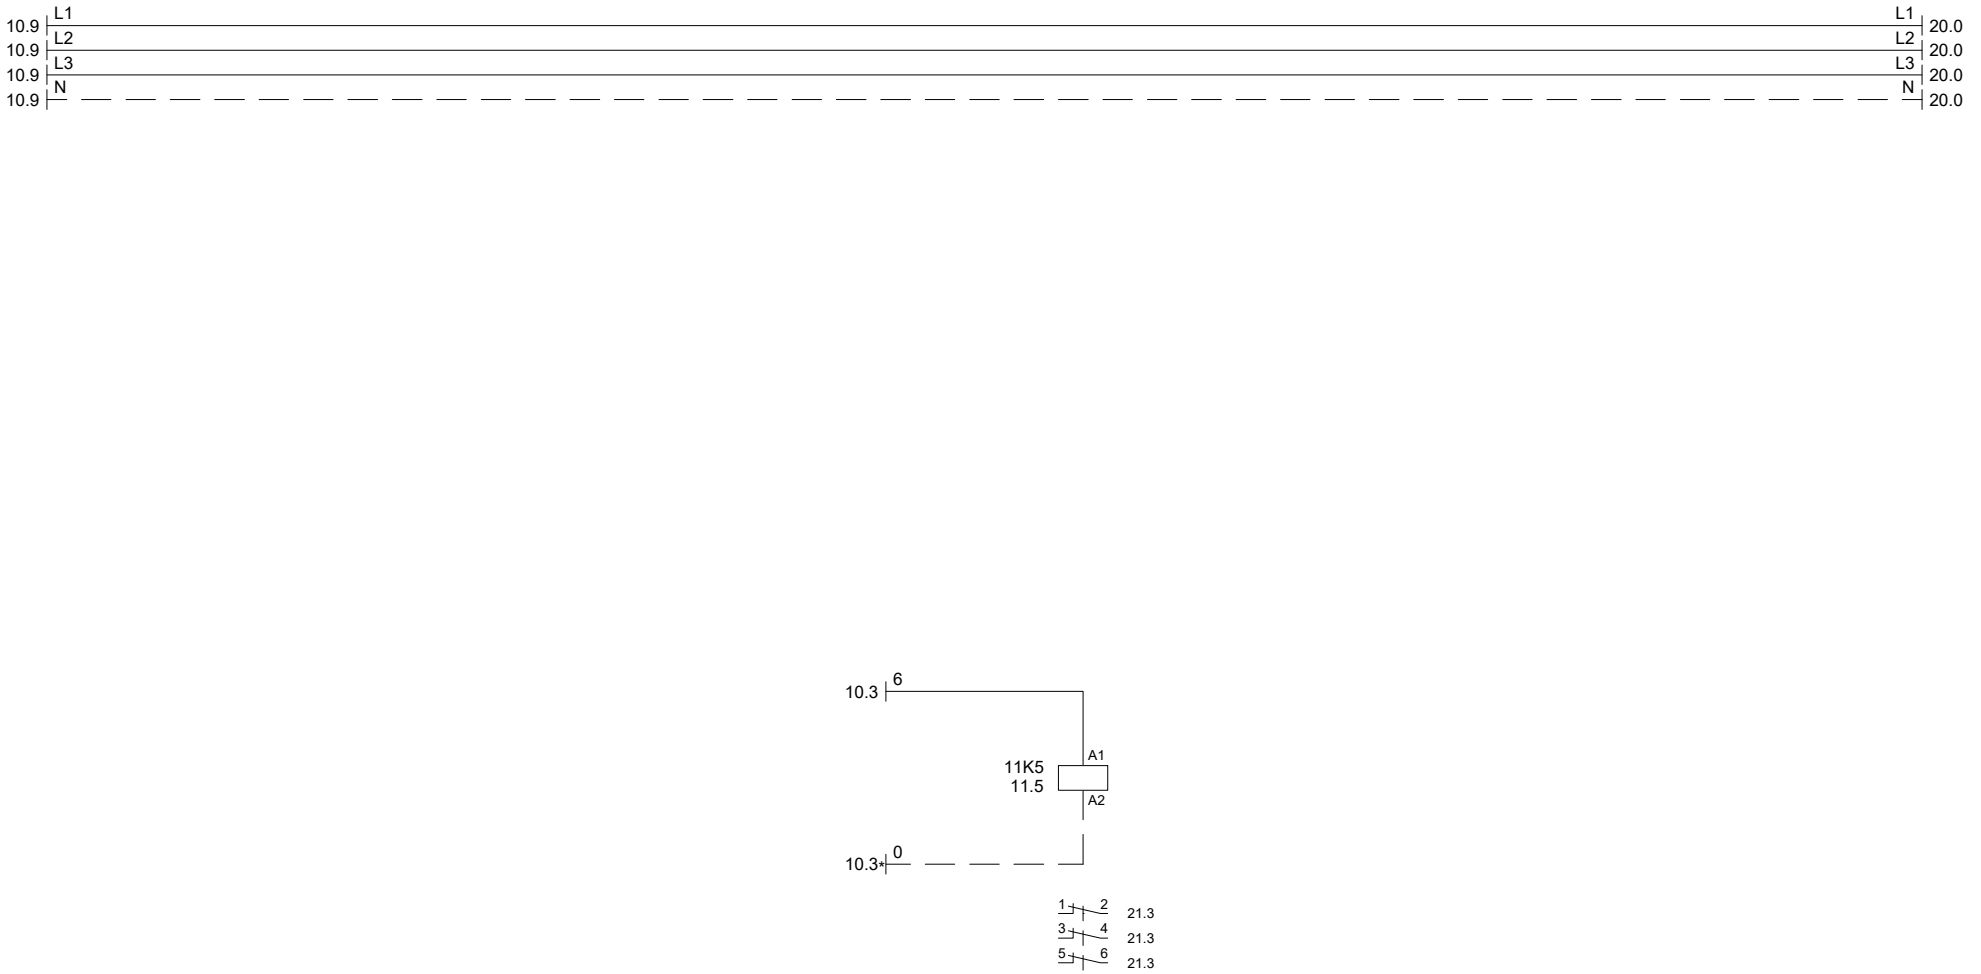

Index	Datum	Name	Gezeichnet
A	09.04.2026	DNO	DNO
			Erstelldatum
			02.11.2025

Hauptverteilung
Wohnung B


ansoplan
elektro-engineering

EVU, Lastabwurf

Auftrag: 24031
Schema: 001

Seite 11
< 10 | 20 >

TinLine GmbH

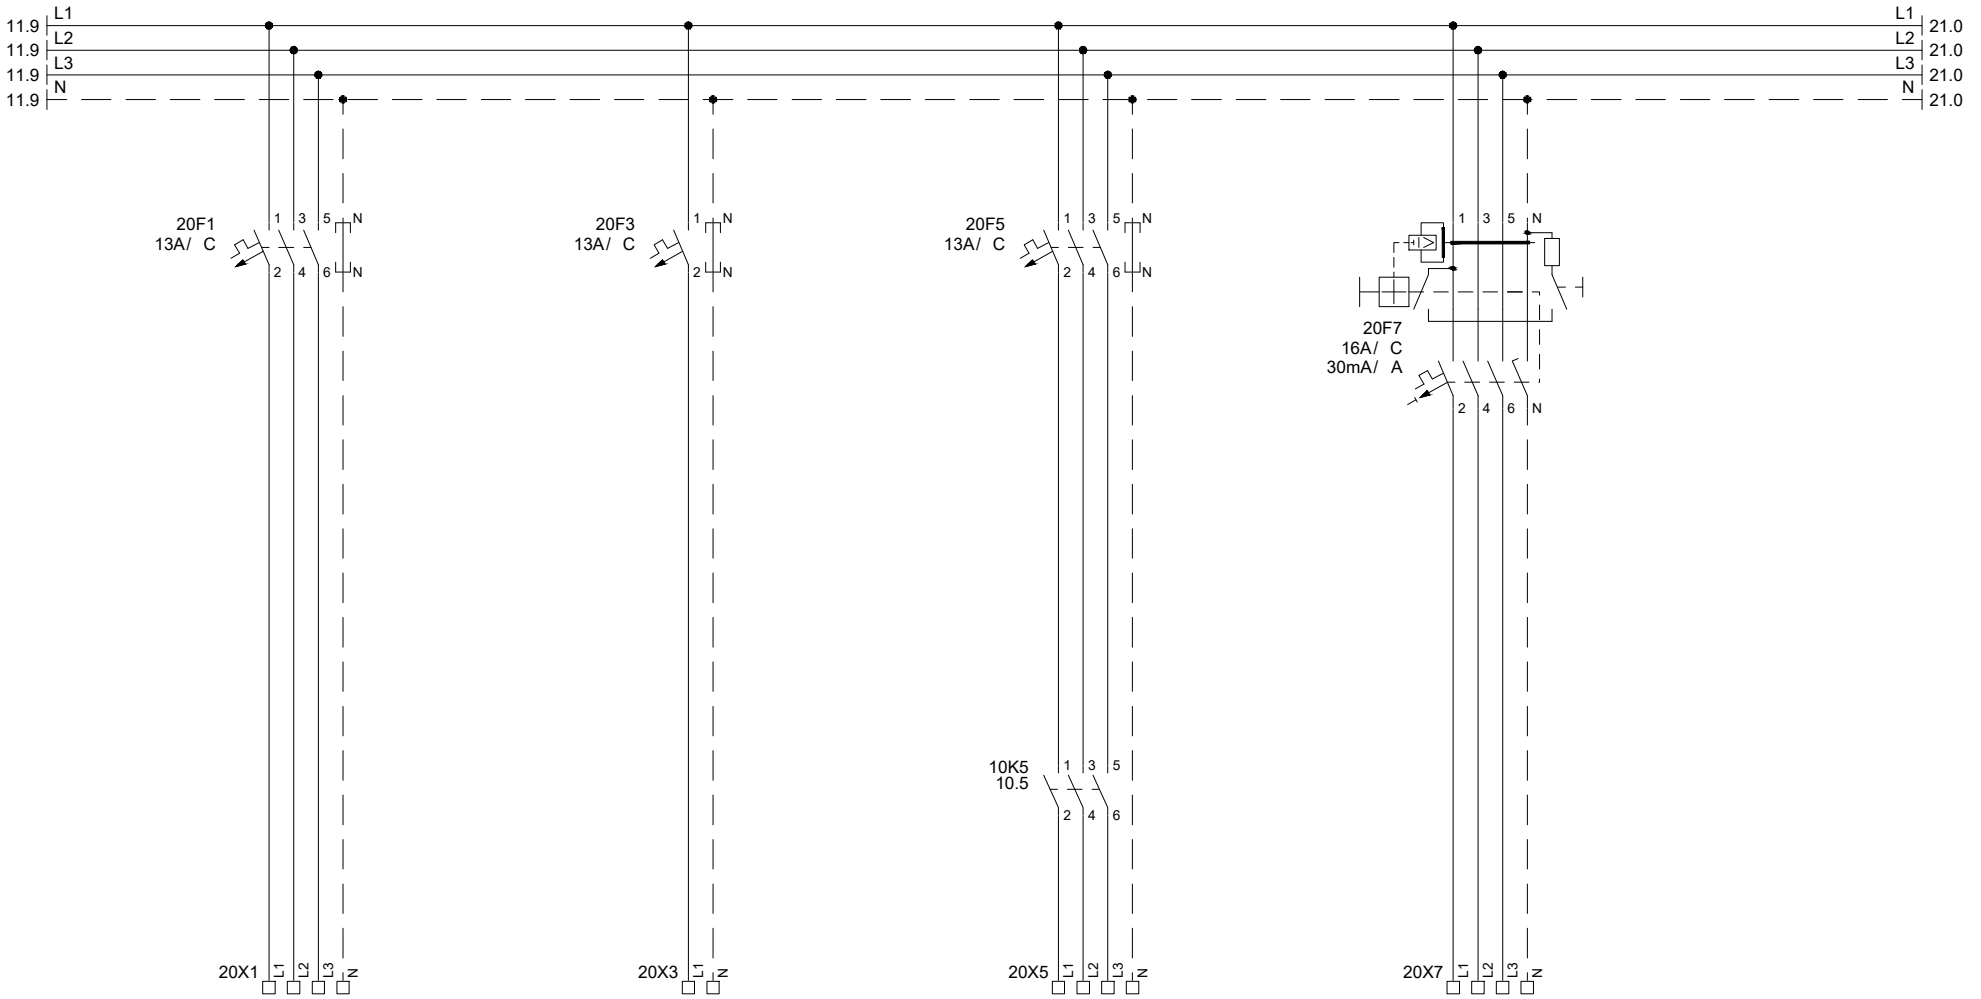

2.5mm²	2.5mm²	2.5mm²	2.5mm²
20X1	20X3	20X5	20X7
L1 L2 L3 N PE	L1 N PE	L1 L2 L3 N PE	L1 L2 L3 N PE
Wärmepumpe	Steuerung Wärmepumpe	Notheizung	Waschmaschine
FE0 5x1.5mm²	FE0 3x1.5mm²	FE0 5x1.5mm²	FE0 5x2.5mm²

Index	Datum	Name	
			Gezeichnet DNO
			Erstelldatum 02.11.2025

Hauptverteilung
Wohnung B


ansoplan
elektro-engineering

Technikraum, Waschmaschine

Auftrag: 24031
Schema: 001

Seite 20
< 11 | 21 >

TinLine GmbH

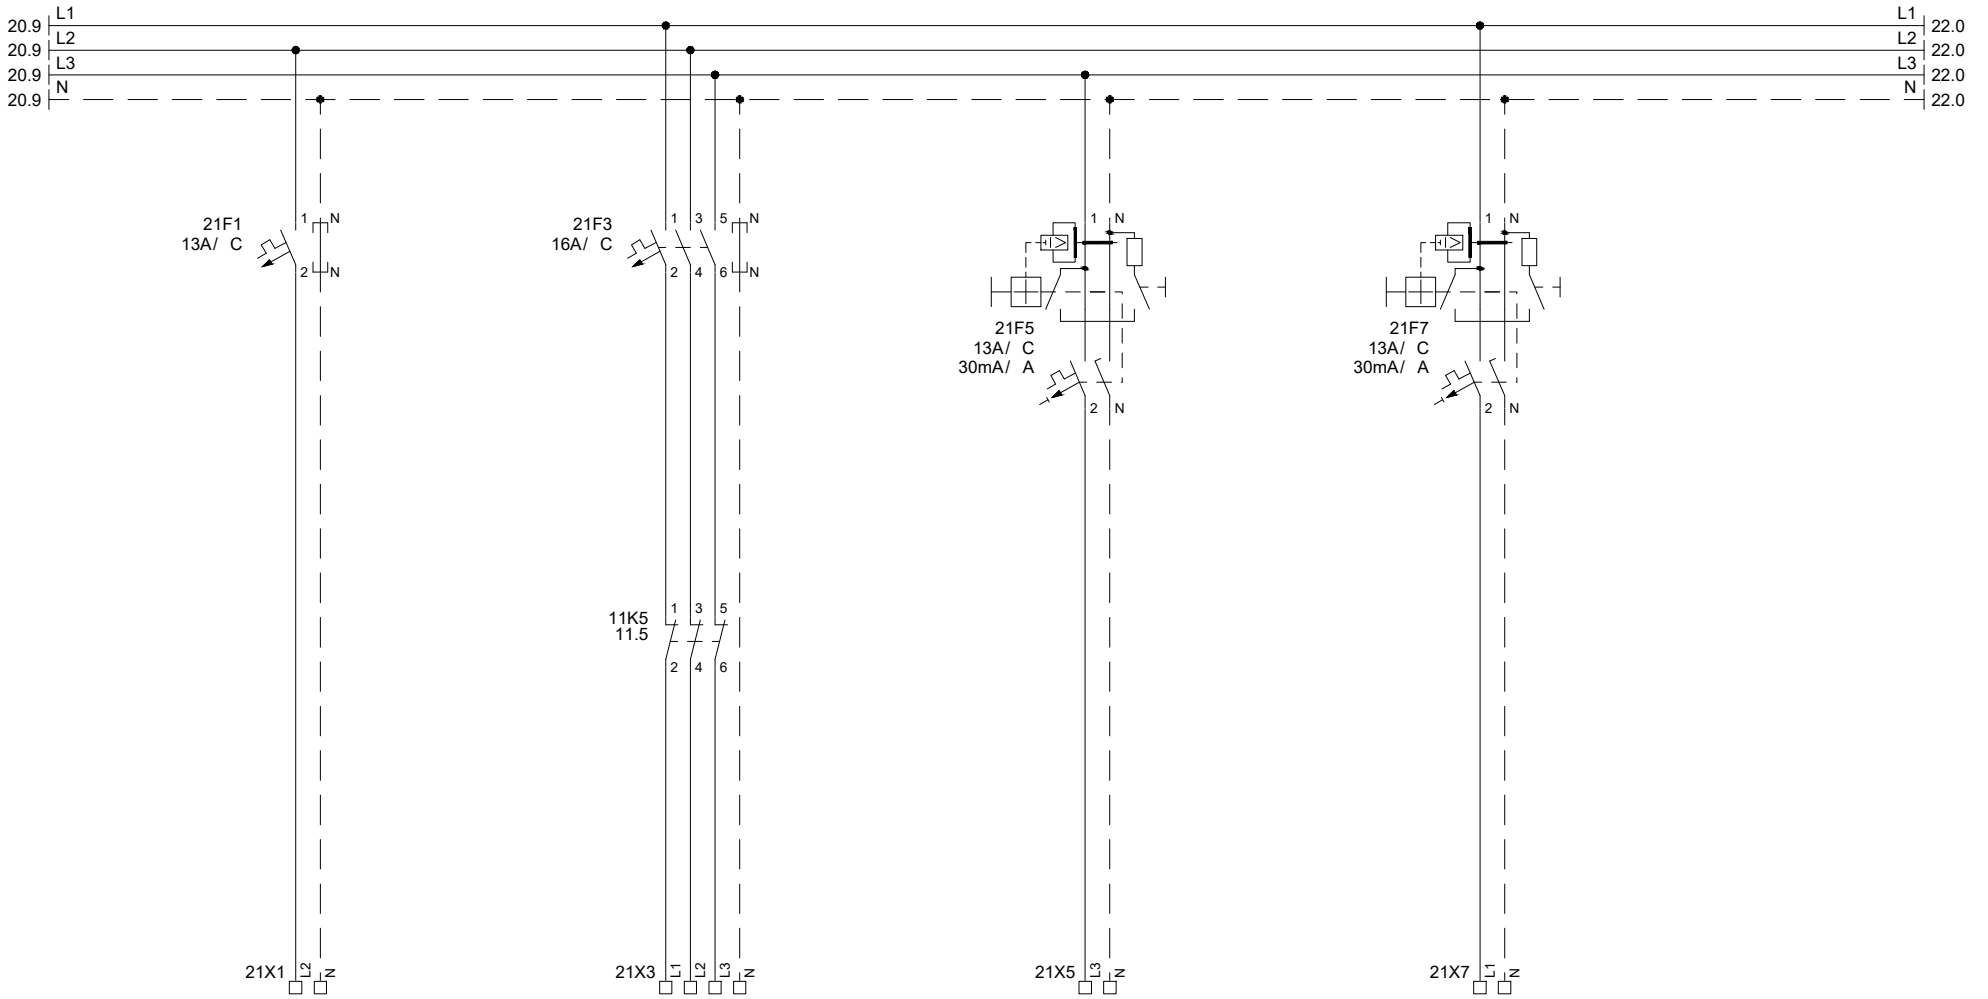

2.5mm²	2.5mm²	2.5mm²	2.5mm²
21X1	21X3	21X5	21X7
L2 N PE	L1 L2 L3 N PE	L3 N PE	L1 N PE
Zirkulationspumpe	Wechselrichter	HZV UG	HZV EG
FE0 3x1.5mm²	FE0 5x2.5mm²	FE0 3x1.5mm²	FE0 3x1.5mm²

Index	Datum	Name	Gezeichnet
A	09.04.2026	DNO	DNO
			Erstelldatum 02.11.2025

Hauptverteilung
Wohnung B


ansoplan elektro-engineering

Technikraum

Auftrag: 24031
Schema: 001

Seite 21
< 20 | 22 >

TinLine GmbH

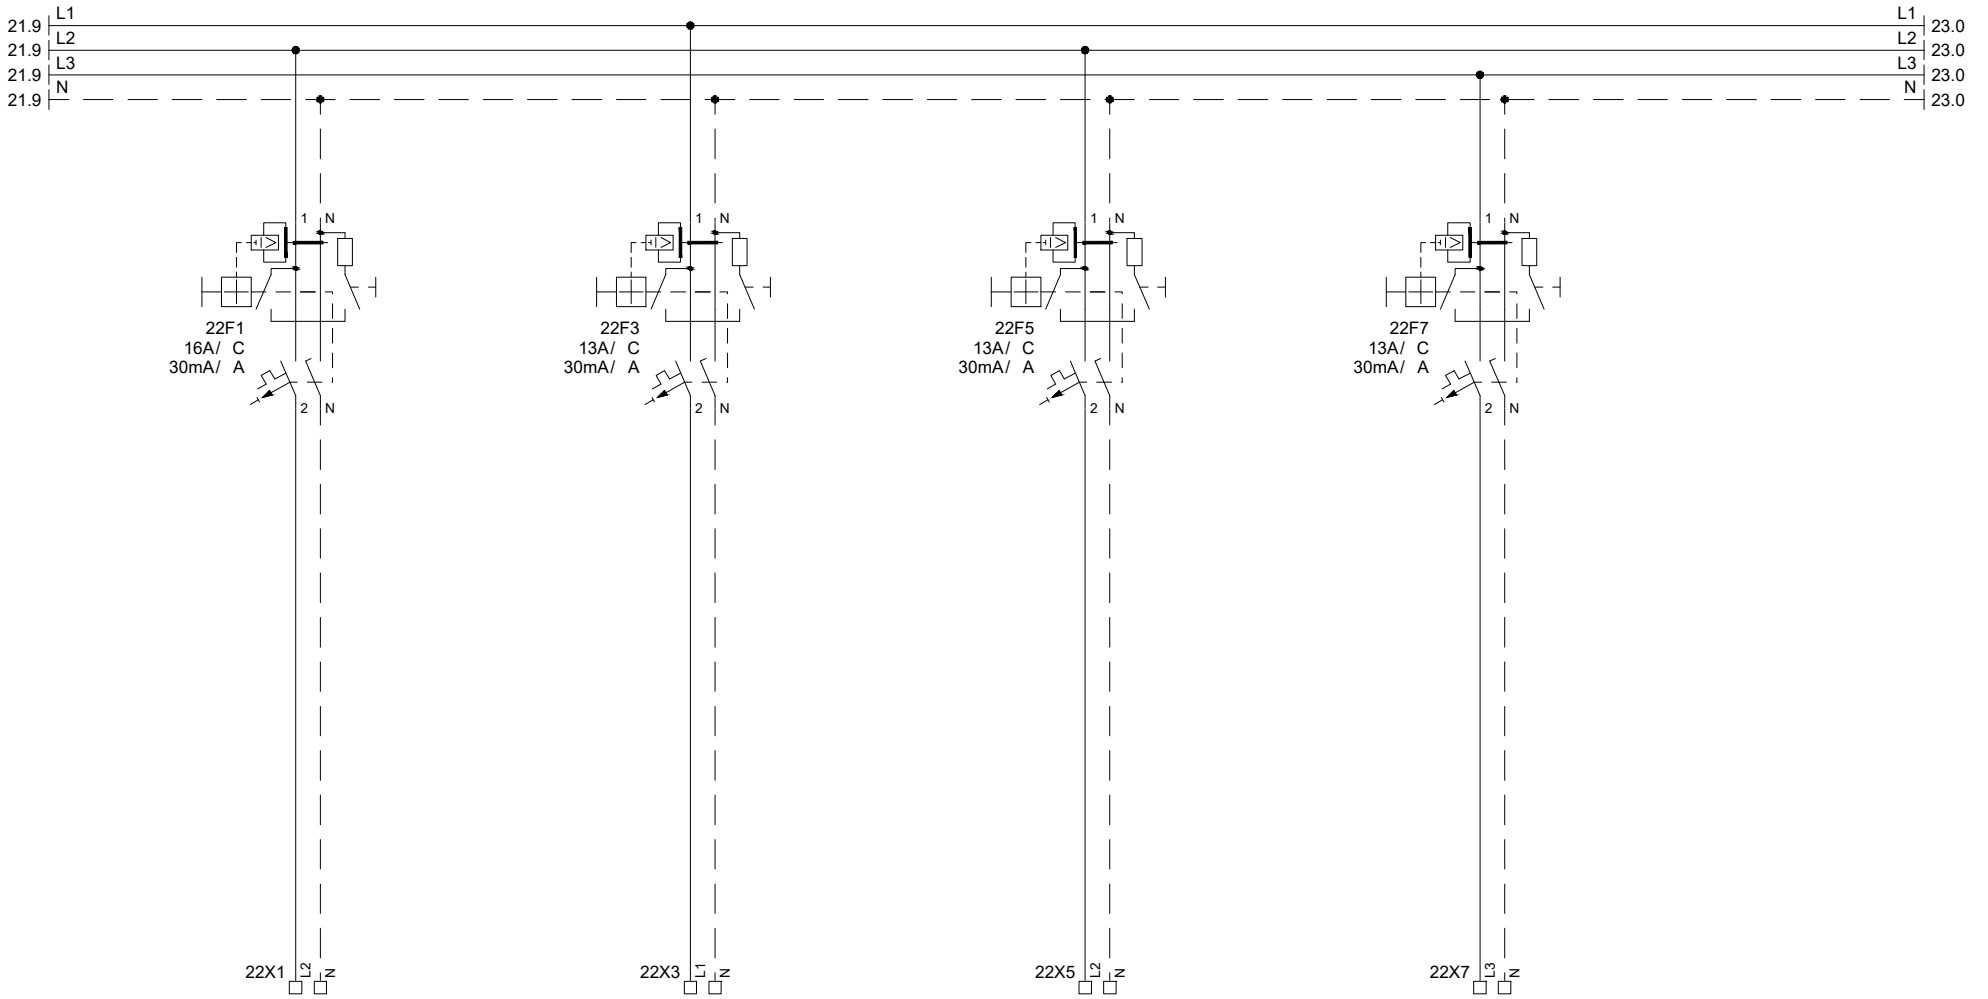

	22X1	22X3	22X5	22X7
	2.5mm²	2.5mm²	2.5mm²	2.5mm²
	L2 N PE	L1 N PE	L2 N PE	L3 N PE
	Tumbler	Schlafzimmer 1+2 UG	Technikraum Keller	Bad, Gang UG
	FE0 3x2.5mm²	FE0 3x1.5mm²	FE0 3x1.5mm²	FE0 3x1.5mm²

Index	Datum	Name	Gezeichnet
			DNO
			Erstelldatum
			02.11.2025

Hauptverteilung
Wohnung B


ansoplan
elektro-engineering

Licht Technikraum, Untergeschoss

Auftrag: 24031
Schema: 001

Seite 22
< 21 | 23 >

TinLine GmbH

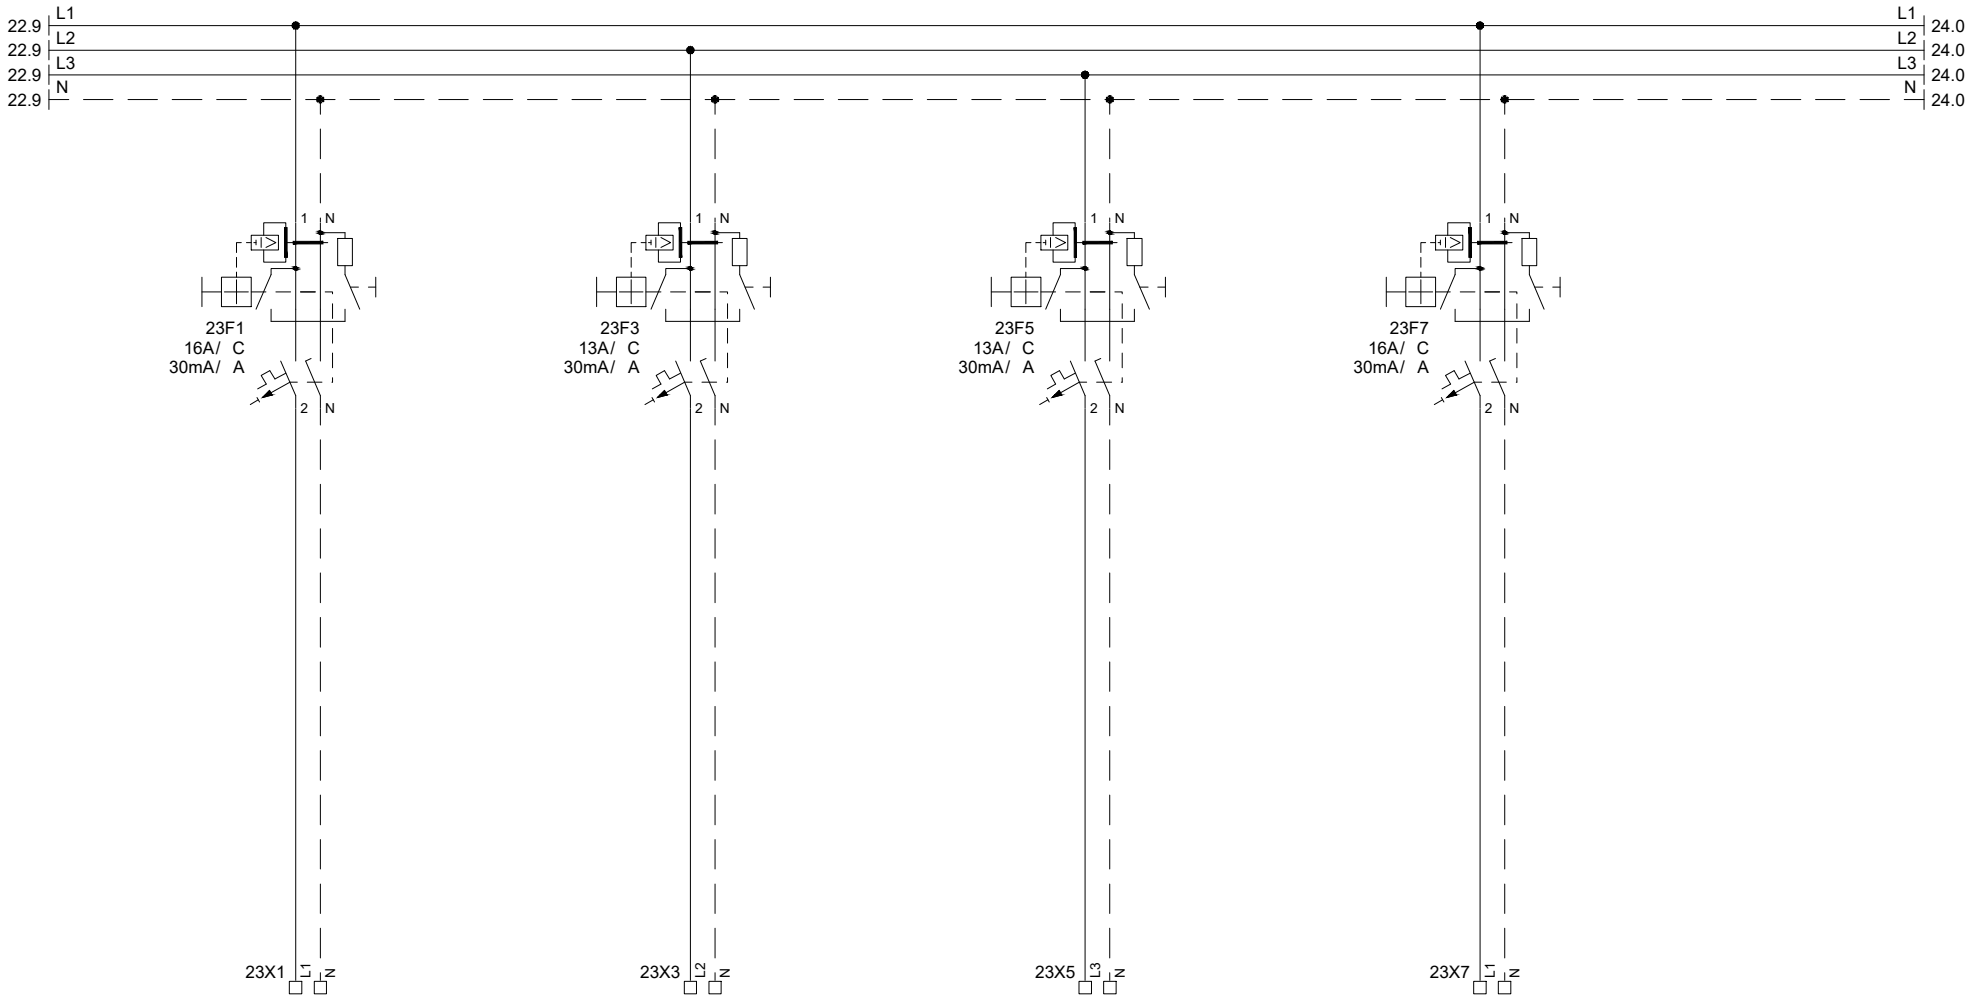

2.5mm²	2.5mm²	2.5mm²	2.5mm²
23X1	23X3	23X5	23X7
L1 N PE	L2 N PE	L3 N PE	L1 N PE
Reserve (Rohrbegleitheizung)	Reserve	Garage	GWA
FE0 3x2.5mm²	FE0 3x1.5mm²	FE0 3x1.5mm²	FE0 3x2.5mm²

Index	Datum	Name	Gezeichnet
			DNO
			Erstelldatum
			02.11.2025

Hauptverteilung
Wohnung B


ansoplan
elektro-engineering

Reserve, Garage, GWA

Auftrag: 24031
Schema: 001

Seite 23
< 22 | 24 >

TinLine GmbH

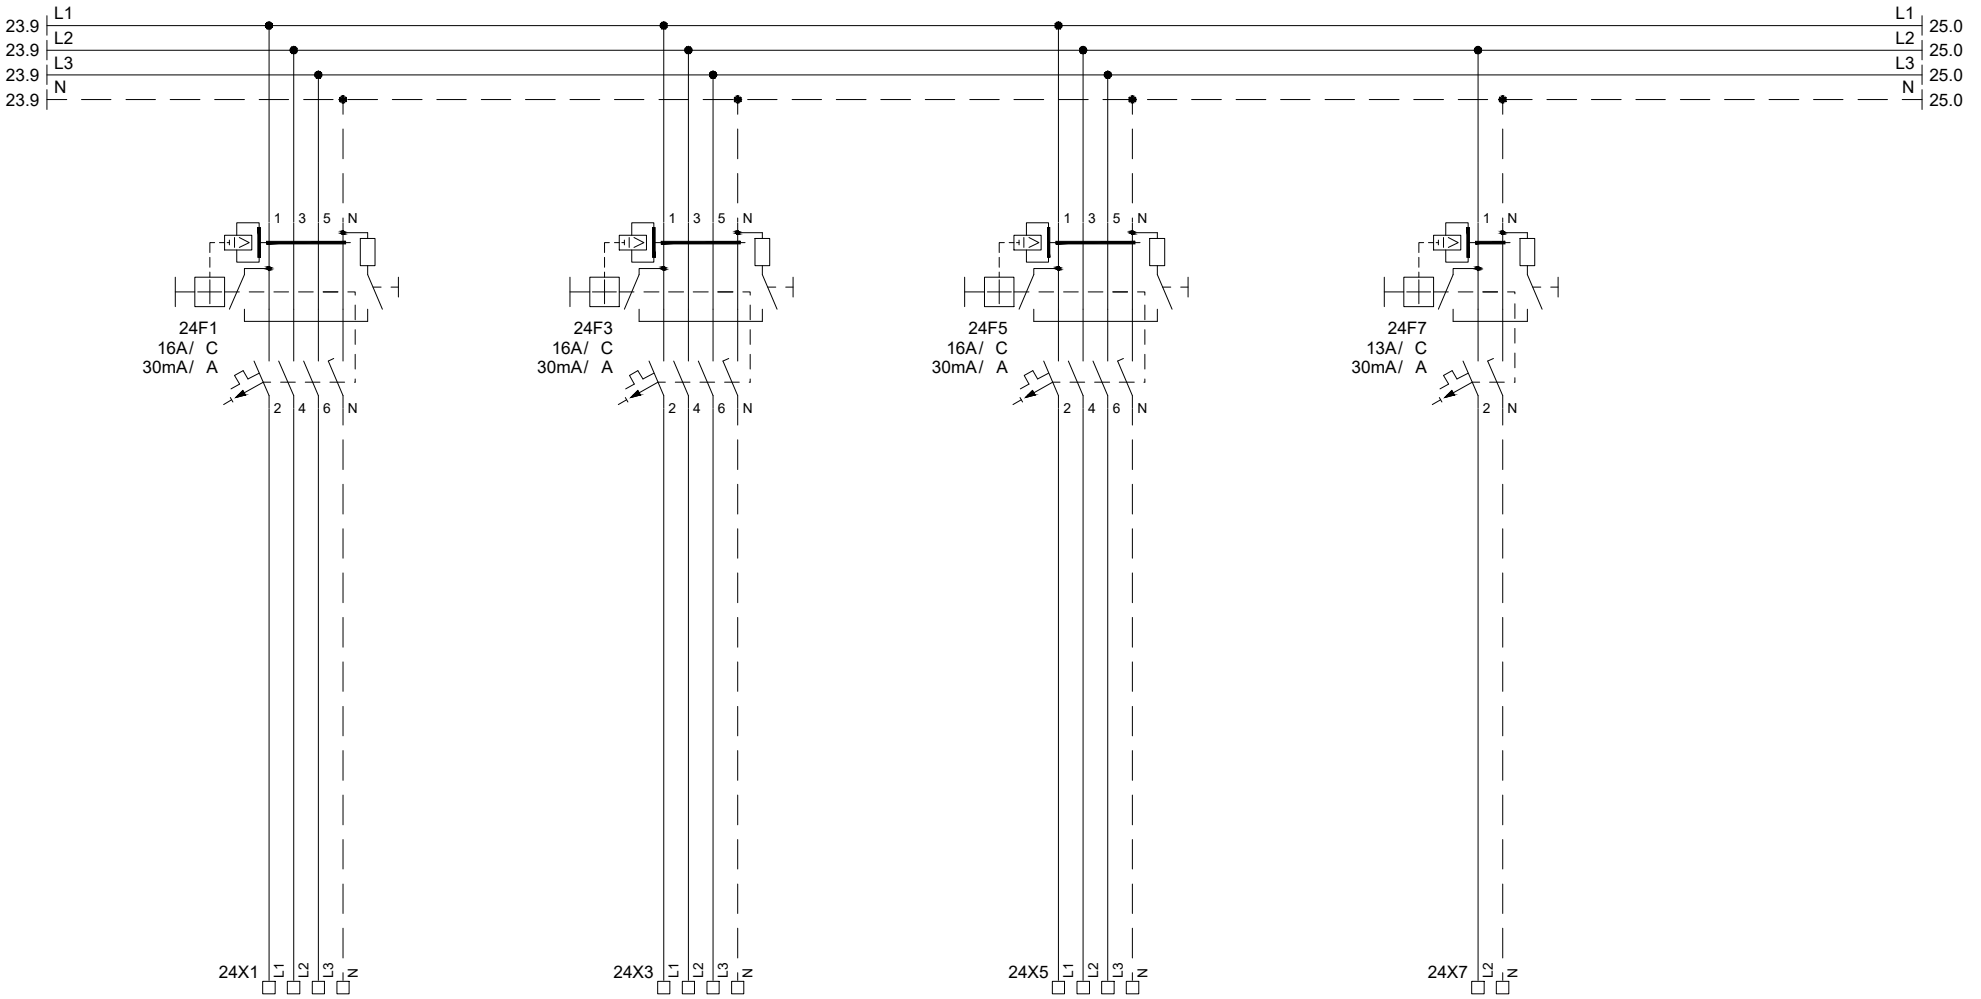

2.5mm²	2.5mm²	2.5mm²	2.5mm²
24X1	24X3	24X5	24X7
L1 L2 L3 N PE	L1 L2 L3 N PE	L1 L2 L3 N PE	L2 N PE
Kochherd	Backofen	Steamer	Wohnzimmer Esszimmer
FE0 5x2.5mm²	FE0 5x2.5mm²	FE0 5x2.5mm²	FE0 3x1.5mm²

Index	Datum	Name	
			Gezeichnet DNO
			Erstelldatum 02.11.2025

Hauptverteilung
Wohnung B


ansoplan elektro-engineering

Kochherd, Backofen, Steamer
Licht Wohnzimmer, Esszimmer

Auftrag: 24031
Schema: 001

Seite 24
< 23 | 25 >

TinLine GmbH

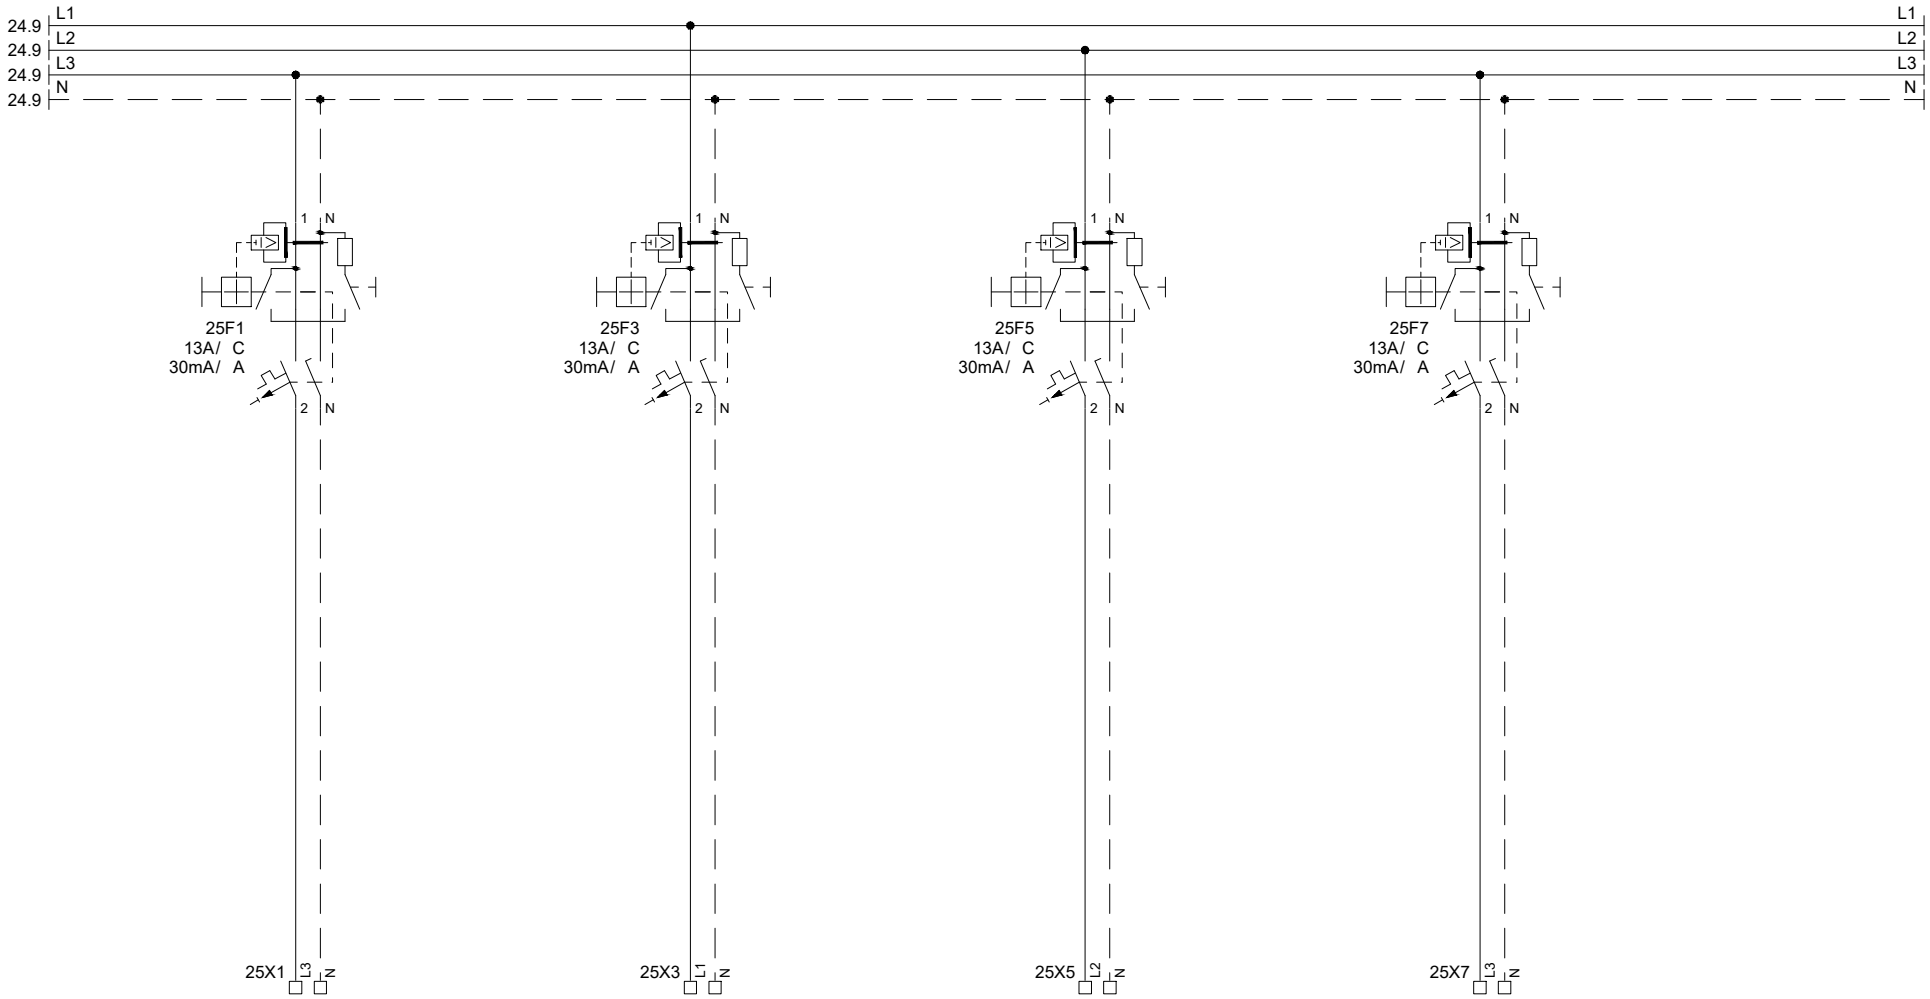

2.5mm²	2.5mm²	2.5mm²	2.5mm²
25X1	25X3	25X5	25X7
L3 N PE	L1 N PE	L2 N PE	L3 N PE
Licht WC, Gang Eingang	Bad OG Gang OG	Schlafzimmer OG	Reserve
FE0 3x1.5mm²	FE0 3x1.5mm²	FE0 3x1.5mm²	FE0 3x1.5mm²

Index	Datum	Name	Gezeichnet
			DNO
			Erstelldatum
			02.11.2025

Hauptverteilung
Wohnung B

ansoplan
elektro-engineering

Licht WC, Schlafzimmer OG

Auftrag: 24031
Schema: 001

Seite 25
< 24 | 1000 >

TinLine GmbH

Kabelliste

BMK	Kabel	Leistung	Bezeichnung / Abgang
10X0	FE0 5x10mm²		Zuleitung ab AZK
10X2	FE0 7x1.5mm²		Klemmen für Tarifdrähte ab NKE AZK Plombierbar
20X1	FE0 5x1.5mm²		Wärmepumpe
20X3	FE0 3x1.5mm²		Steuerung Wärmepumpe
20X5	FE0 5x1.5mm²		Notheizung
20X7	FE0 5x2.5mm²		Waschmaschine
21X1	FE0 3x1.5mm²		Zirkulationspumpe
21X3	FE0 5x2.5mm²		Wechselrichter
21X5	FE0 3x1.5mm²		HZV UG
21X7	FE0 3x1.5mm²		HZV EG
22X1	FE0 3x2.5mm²		Tumbler
22X3	FE0 3x1.5mm²		Schlafzimmer 1+2 UG
22X5	FE0 3x1.5mm²		Technikraum Keller
22X7	FE0 3x1.5mm²		Bad, Gang UG
23X1	FE0 3x2.5mm²		Reserve (Rohrbegleitheizung)
23X3	FE0 3x1.5mm²		Reserve
23X5	FE0 3x1.5mm²		Garage
23X7	FE0 3x2.5mm²		GWA
24X1	FE0 5x2.5mm²		Kochherd
24X3	FE0 5x2.5mm²		Backofen
24X5	FE0 5x2.5mm²		Steamer
24X7	FE0 3x1.5mm²		Wohnzimmer Esszimmer
25X1	FE0 3x1.5mm²		Licht WC, Gang Eingang
25X3	FE0 3x1.5mm²		Bad OG Gang OG
25X5	FE0 3x1.5mm²		Schlafzimmer OG

Klemmenliste

BMK	Kabel	Bezeichnung / Abgang	1	2	3	4	5	6	7	8	9	10
10X0	FE0 5x10mm²	Zuleitung ab AZK	L1	L2	L3	N	PE					
10X2	FE0 7x1.5mm²	Klemmen für Tarifdrähte ab NKE AZK Plombierbar	1	2	3	4	5	6	0			
20X1	FE0 5x1.5mm²	Wärmepumpe	L1	L2	L3	N	PE					
20X3	FE0 3x1.5mm²	Steuerung Wärmepumpe	L1	N	PE							
20X5	FE0 5x1.5mm²	Notheizung	L1	L2	L3	N	PE					
20X7	FE0 5x2.5mm²	Waschmaschine	L1	L2	L3	N	PE					
21X1	FE0 3x1.5mm²	Zirkulationspumpe	L2	N	PE							
21X3	FE0 5x2.5mm²	Wechselrichter	L1	L2	L3	N	PE					
21X5	FE0 3x1.5mm²	HZV UG	L3	N	PE							
21X7	FE0 3x1.5mm²	HZV EG	L1	N	PE							
22X1	FE0 3x2.5mm²	Tumbler	L2	N	PE							
22X3	FE0 3x1.5mm²	Schlafzimmer 1+2 UG	L1	N	PE							
22X5	FE0 3x1.5mm²	Technikraum Keller	L2	N	PE							
22X7	FE0 3x1.5mm²	Bad, Gang UG	L3	N	PE							
23X1	FE0 3x2.5mm²	Reserve (Rohrbegleitheizung)	L1	N	PE							
23X3	FE0 3x1.5mm²	Reserve	L2	N	PE							
23X5	FE0 3x1.5mm²	Garage	L3	N	PE							
23X7	FE0 3x2.5mm²	GWA	L1	N	PE							
24X1	FE0 5x2.5mm²	Kochherd	L1	L2	L3	N	PE					
24X3	FE0 5x2.5mm²	Backofen	L1	L2	L3	N	PE					
24X5	FE0 5x2.5mm²	Steamer	L1	L2	L3	N	PE					
24X7	FE0 3x1.5mm²	Wohnzimmer Esszimmer	L2	N	PE							
25X1	FE0 3x1.5mm²	Licht WC, Gang Eingang	L3	N	PE							
25X3	FE0 3x1.5mm²	Bad OG Gang OG	L1	N	PE							
25X5	FE0 3x1.5mm²	Schlafzimmer OG	L2	N	PE							